
Nuova disposizione: pianta quotata, scala 1:100

Stessi ambienti e stesso perimetro della casa di Zanuso. Stampa in A3 al 100% e il lato della casa misura 156 mm.

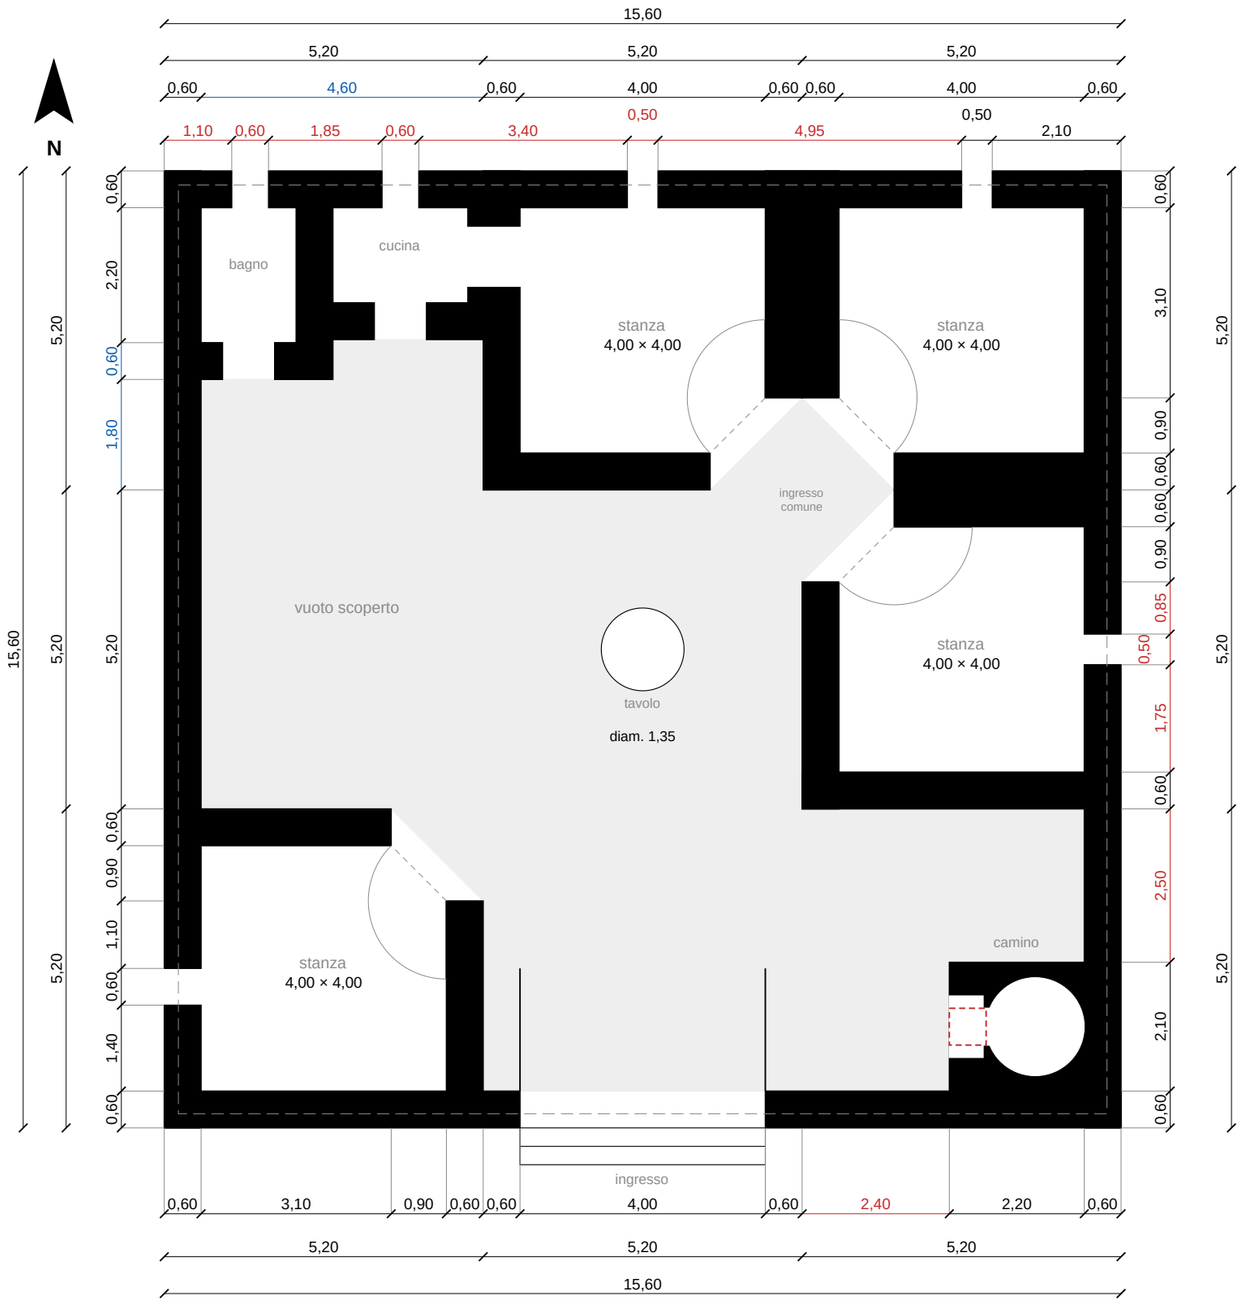

Le quattro porte delle stanze (X da ovest, Y da nord)

Porta	Muro che si interrompe	Altro muro	Larghezza
In alto al centro	sud a X = 8,90	est a Y = 3,70	1,27
In alto a destra	sud a X = 11,90	ovest a Y = 3,70	1,27
Sul lato est	nord a X = 11,90	ovest a Y = 6,70	1,27
In basso a sinistra	nord a X = 3,70	est a Y = 11,90	1,27

Le sei finestre

Finestra	Posizione	Larg.	Da / a sul pav.
Bagno, muro nord	X da 1,10 a 1,70	0,60	1,05 - 1,70
Cucina, muro nord	X da 3,55 a 4,15	0,60	1,05 - 1,70
Stanza in alto al centro, nord	X da 7,55 a 8,05	0,50	1,05 - 1,70
Stanza in alto a destra, nord	X da 13,00 a 13,50	0,50	1,05 - 1,70
Stanza sul lato est, est	Y da 7,55 a 8,05	0,50	1,05 - 1,70
Stanza in basso a sin., ovest	Y da 13,00 a 13,60	0,60	1,05 - 1,70

Altezze e ingresso

Altezze	Metri	Plastico (mm)
Muri, sul pavimento	3,30	33
Rialzo della casa sul terreno	0,40	4
Porte delle stanze	2,10	21
Ingresso a sud, larghezza × altezza	4,00 × 2,00	40 × 20
Architrave dell'ingresso, lungo × alto	5,70 × 0,45	57 × 4,5
Due gradini fuori dall'ingresso, alti e profondi	0,20 e 0,30	2 e 3

Come leggere le quote (in metri)

nero: misura della casa vera

blu: posizione presa dal tuo schizzo

rosso: scelta mia, nello schizzo non c'è: puoi cambiarla

Sul plastico in scala 1:100: moltiplica per 10 e leggi millimetri (1,50 m = 15 mm).


Tratteggio esterno: filo del muro in cima (i muri esterni sono inclinati). Grigio: vuoto scoperto. Tratteggio rosso sul camino: canna fumaria.

I muri tra stanze vicine sono doppi (0,60 + 0,60 = 1,20), perché ogni stanza tiene i suoi muri come nella griglia di Zanuso.


Nuova disposizione: i dettagli

Ingresso comune delle tre stanze 1:25, bagno e cucina 1:50, camino 1:50.


Ingresso comune delle tre stanze, 1:25

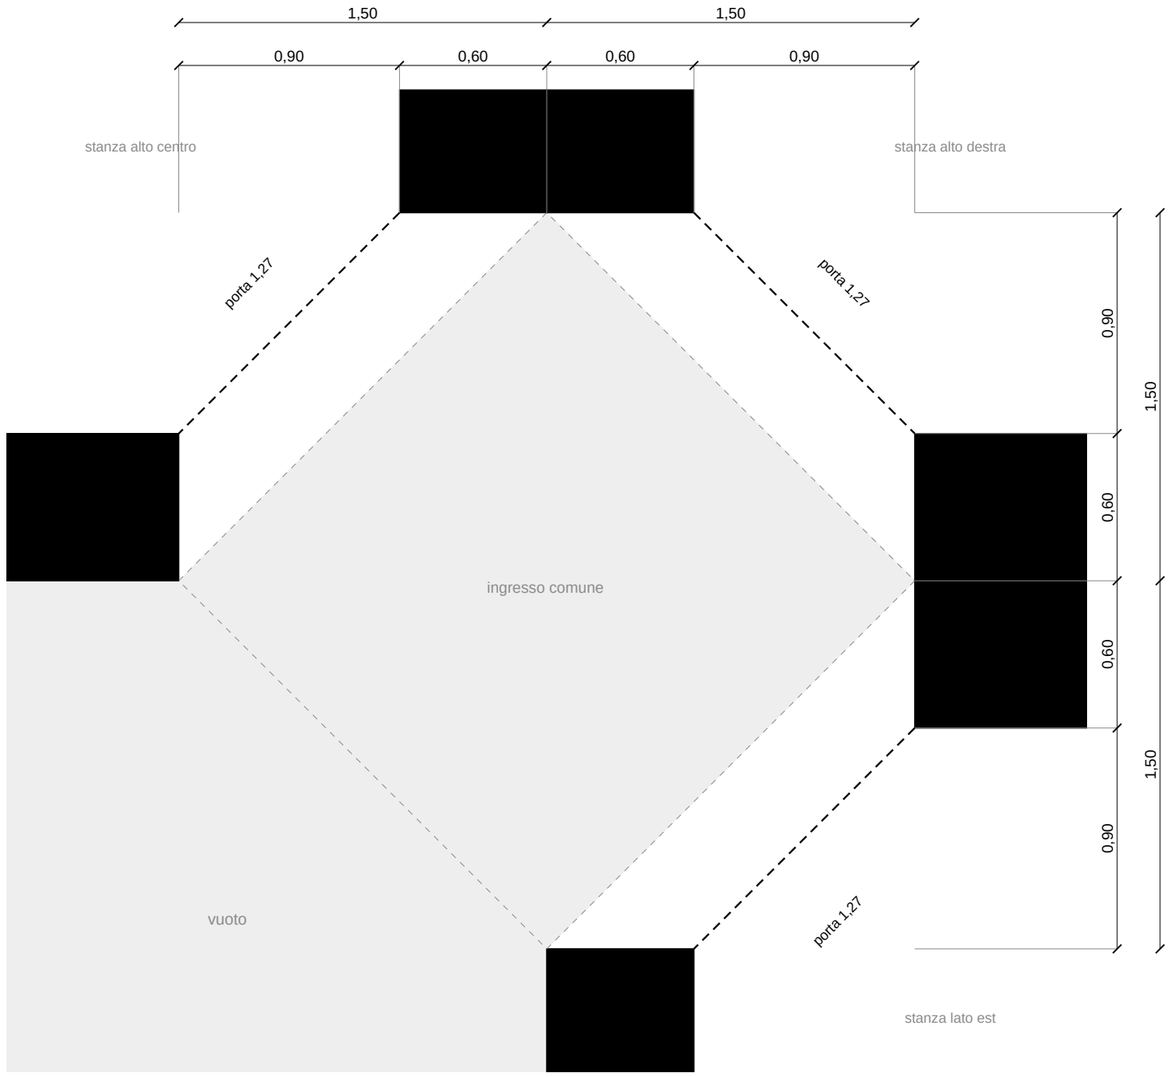

Bagno e cucina, 1:50

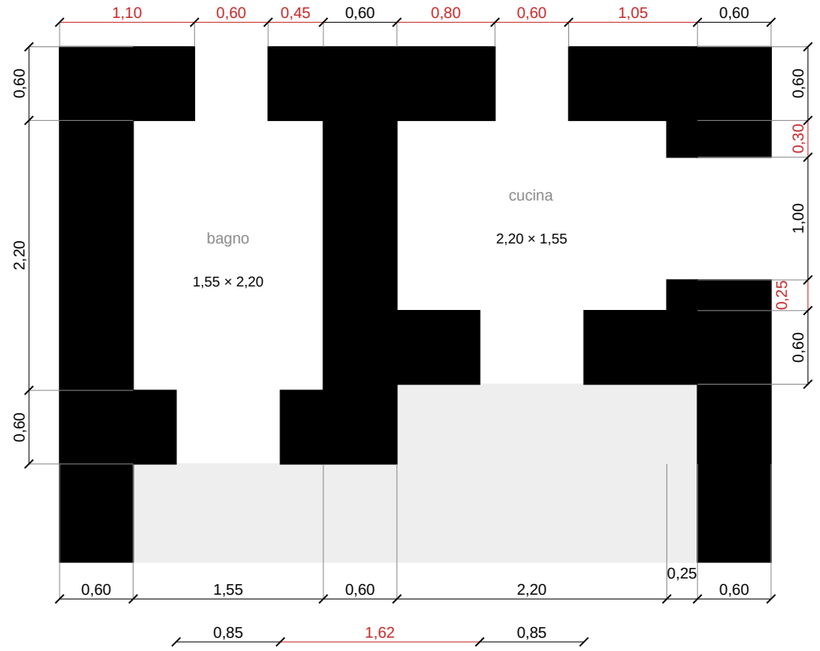

Camino, 1:50 (senza la nicchia esterna, nell'angolo sud-est)

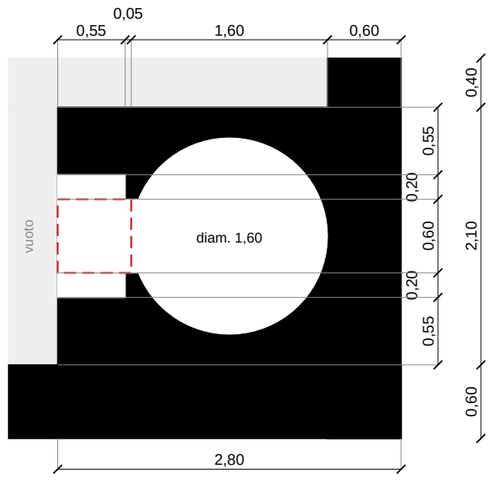

Camino	Metri	mm
Blocco largo	2,10	21
Dal bordo est	2,80	28
Altezza blocco	3,20	32
Bocca, larga	1,00	10
Canna fumaria	0,60 × 0,60	6 × 6
Sopra il tetto	1,85	18,5

Ogni muro si ferma a 1,50 m dall'angolo in cui si incontrano le tre stanze, come nella casa vera. L'angolo sta a X = 10,40 e Y = 5,20: sul plastico a 104 mm dal bordo ovest e 52 mm dal bordo nord. Le porte sono alte 2,10 m: sopra, i muri continuano fino all'angolo, quindi l'ingresso comune resta coperto.

Come leggere le quote (in metri)

nero: misura della casa vera

blu: posizione presa dal tuo schizzo

rosso: scelta mia, nello schizzo non c'è: puoi cambiarla

Sul plastico in scala 1:100: moltiplica per 10 e leggi millimetri (1,50 m = 15 mm).

La bocca guarda a ovest, verso l'ingresso. Il blocco tocca i muri est e sud: da 129 a 150 mm dal bordo nord. Ho tolto nicchia esterna e muro dietro: le altezze restano quelle della tavola 4 della casa vera.

Bagno e cucina hanno le misure della casa vera. Nel tuo schizzo il bagno era più profondo: con le misure vere davanti resta una striscia di vuoto. Il muro est della cucina è spesso 0,85: sul plastico bastano 2 strati di Poliplat.

Il passaggio tra cucina e stanza è largo 1,00, con altezza 2,10 (scelta mia).