
Pianta quotata, scala 1:100

Pianta tagliata all'altezza delle finestre. Stampa in A3 al 100% e il lato della casa misura 156 mm.

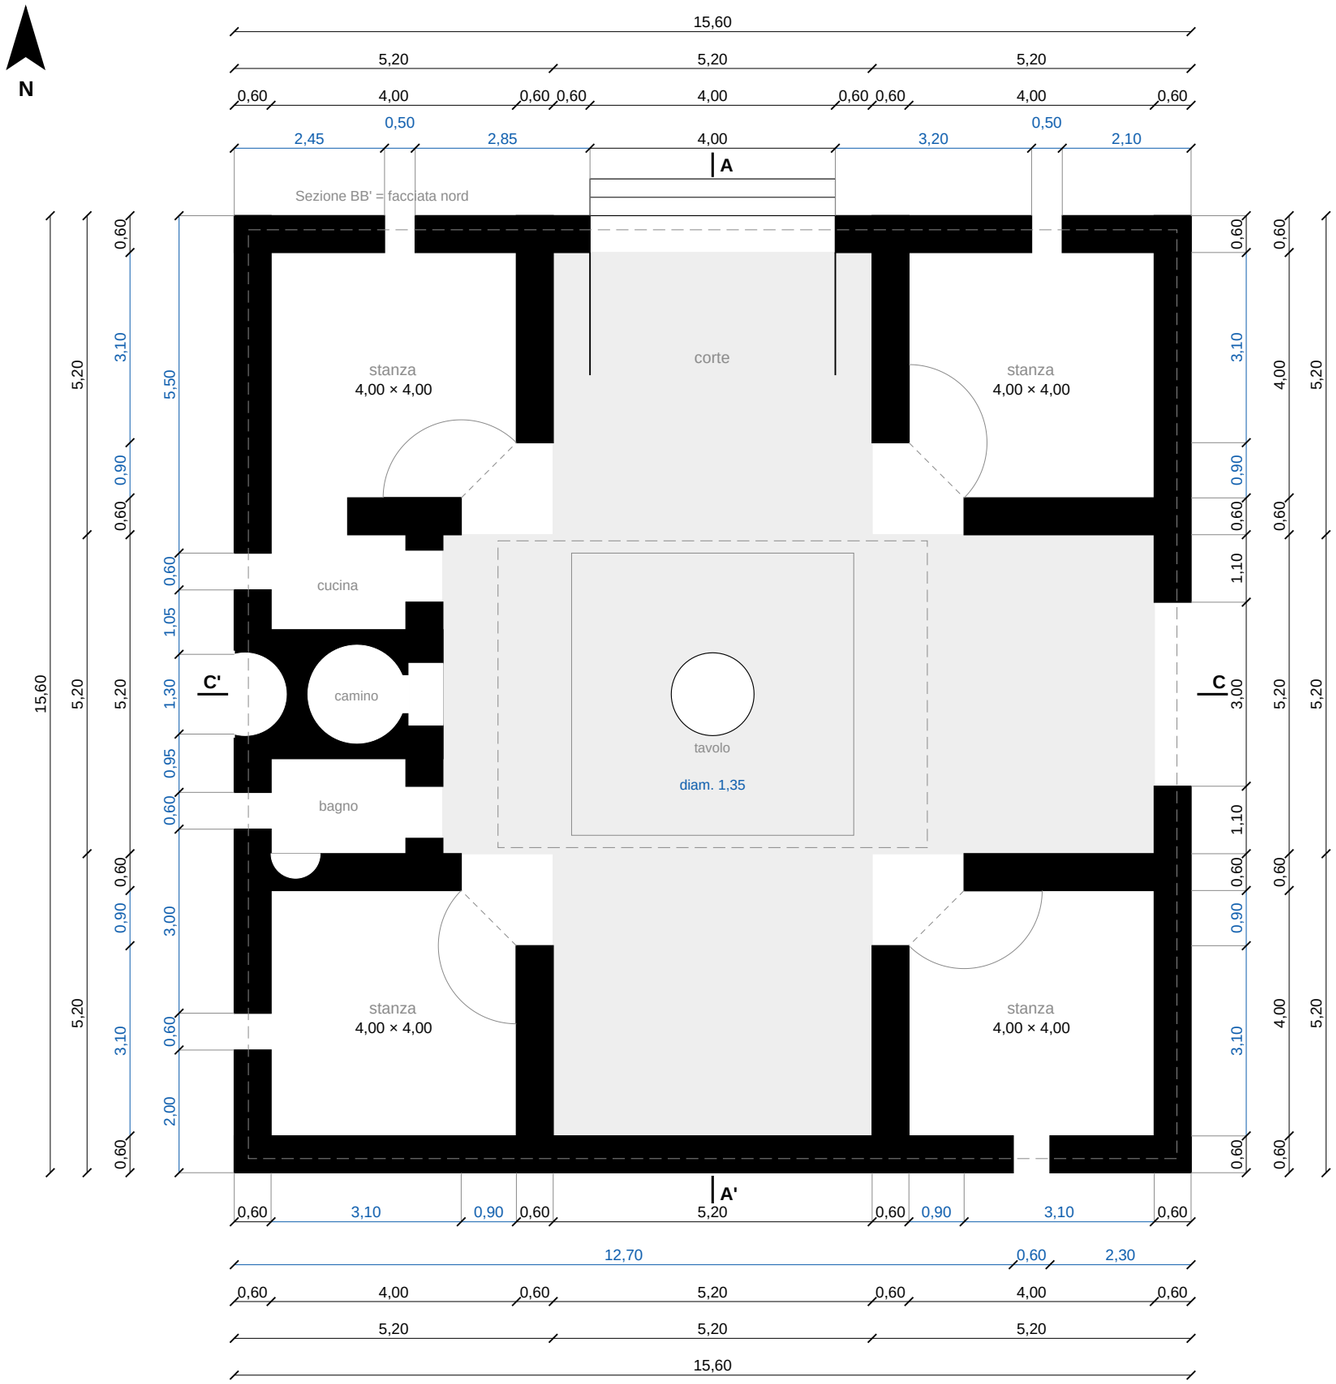


Tratteggio esterno: filo del muro in cima (i muri esterni sono inclinati).

Tratteggio nella corte: copertura leggera. Linee spesse nel braccio nord: le due ante aperte.

Il quadrato sottile nella corte è la pavimentazione (4,60 × 4,60), il cerchio è il tavolo.

Dettaglio di una porta (angolo nord-ovest), 1:25

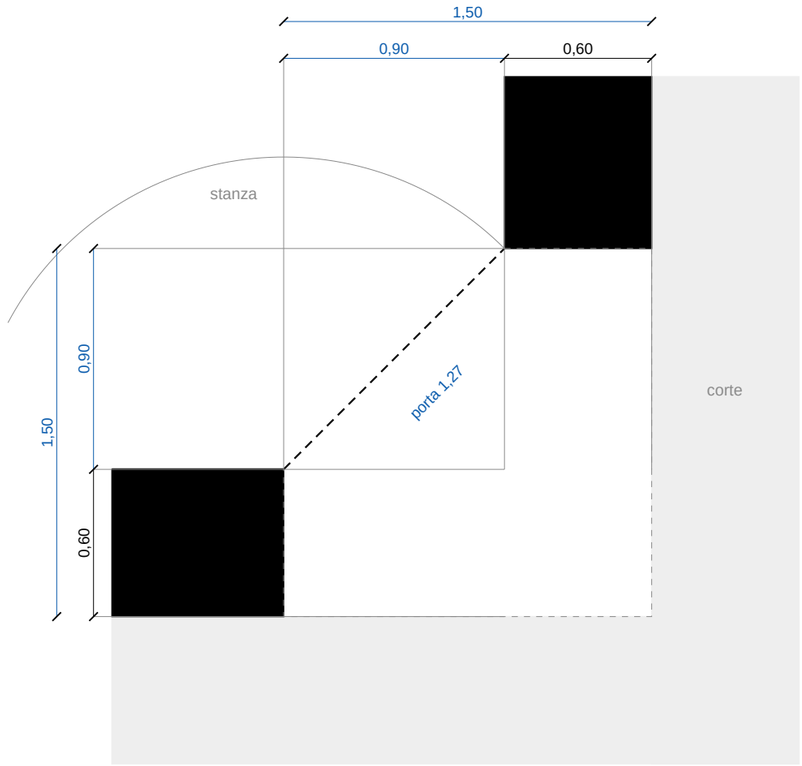

Ogni muro si ferma a 1,50 m dall'angolo della croce: 0,90 m liberi dentro la stanza + 0,60 m di spessore. La porta è in diagonale tra le due punte di muro, larga 1,27 m, anta verso la stanza. Sopra 2,10 m il muro continua fino all'angolo della croce (linea sottile tratteggiata).

Le quattro porte (X da ovest, Y da nord)

Porta	Il muro est-ovest finisce	Il pilastro nord-sud finisce	Cardine
NO	a X = 3,70	a Y = 3,70	sulla punta del muro
NE	a X = 11,90	a Y = 3,70	sulla punta del pilastro
SO	a X = 3,70	a Y = 11,90	sulla punta del pilastro
SE	a X = 11,90	a Y = 11,90	sulla punta del muro

Le sei finestre

Finestra	Posizione	Larg.	Da / a sul pavimento
Nord, stanza NO	X da 2,45 a 2,95	0,50	1,05 - 1,70
Nord, stanza NE	X da 13,00 a 13,50	0,50	1,05 - 1,70
Sud, stanza SE	X da 12,70 a 13,30	0,60	1,05 - 1,70
Ovest, cucina	Y da 5,50 a 6,10	0,60	1,05 - 1,70
Ovest, bagno	Y da 9,40 a 10,00	0,60	1,05 - 1,70
Ovest, stanza SO	Y da 13,00 a 13,60	0,60	1,05 - 1,70

Come leggere le quote (in metri)

nero: scritta sulla scheda del prof

blu: misurata sul disegno della scheda (margine circa 5-10 cm)


rosso: ipotesi, la scheda non la dice: da chiedere al prof

Sul plastico in scala 1:100: moltiplica per 10 e leggi millimetri (1,50 m = 15 mm).

Fascia ovest e camino, scale 1:50 e 1:25

Dove stanno cucina, camino e bagno, e tutte le misure del camino in pianta. Cucina e bagno nel dettaglio: tavola 3.

Pianta della fascia ovest, 1:50

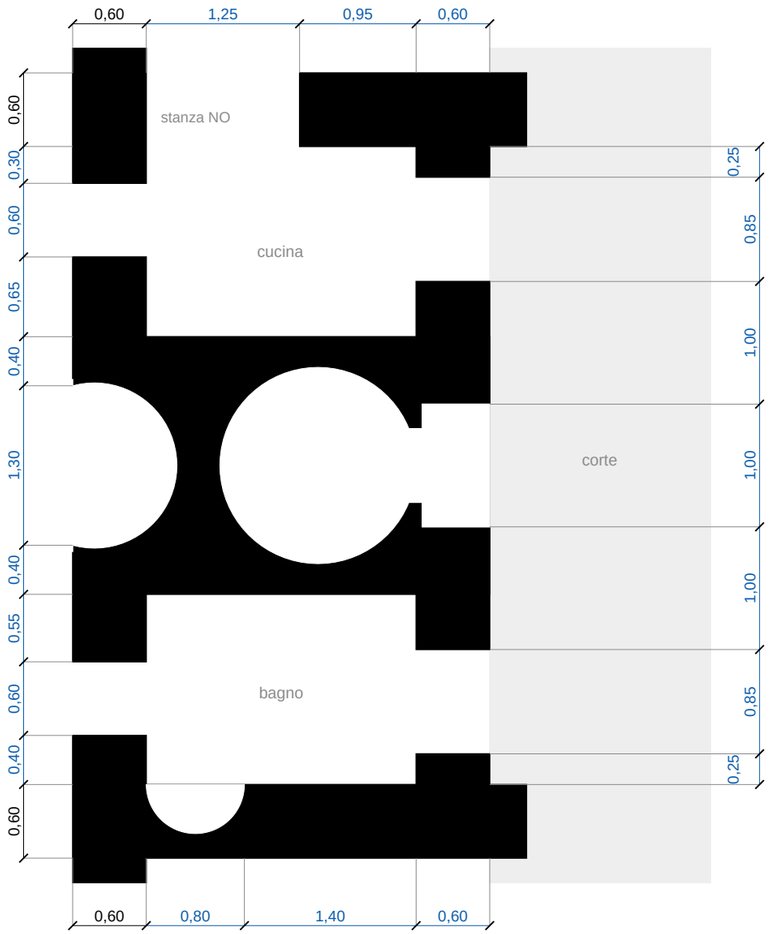


Aperture sulla corte: cucina 0,85; camino 1,00; bagno 0,85.

Altezza di cucina e bagno: 2,10 (ipotesi, come le porte).

Nicchia nel bagno: larga 0,80, profonda 0,40.

Camino in pianta, 1:25

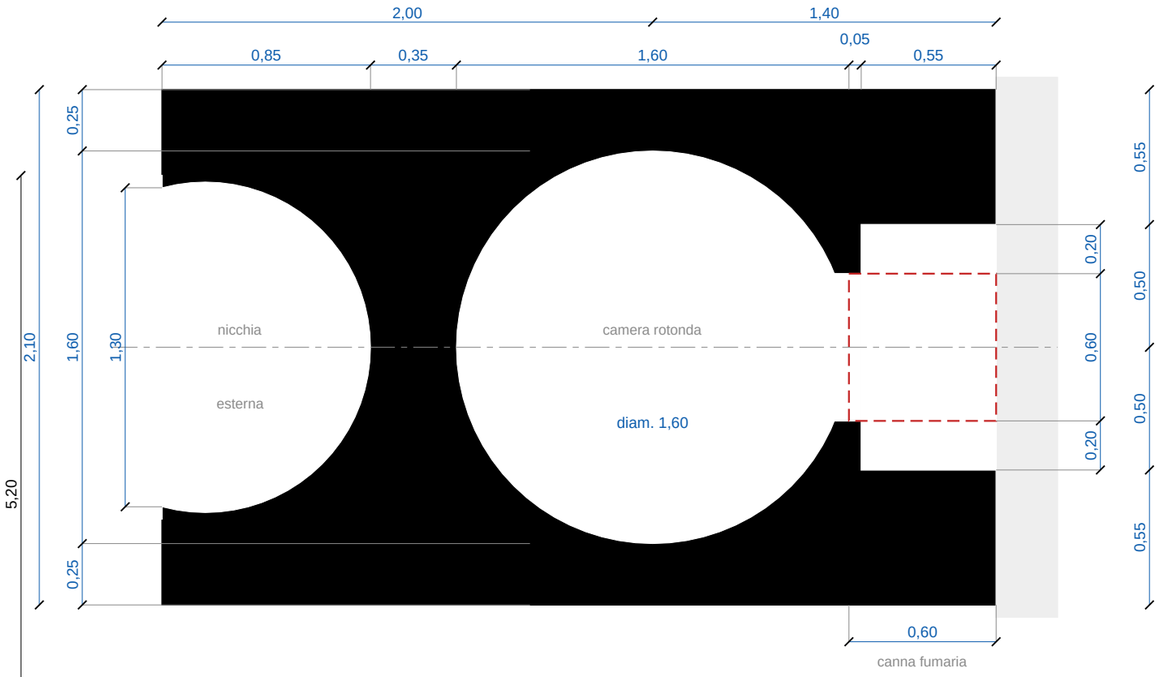

Rosso tratteggiato: canna fumaria in pianta. La scheda la mostra solo da un lato (0,60); la profondità nord-sud 0,60 è un'ipotesi: canna quadrata, centrata sull'asse del camino.

Camino: cosa	Metri	Plastico (mm)
Blocco, dal filo ovest alla corte × nord-sud	3,40 × 2,10	34 × 21
Altezza del blocco sul pavimento	3,20	32
Muro tra nicchia esterna e camera	0,35	3,5
Camera rotonda, diametro (centro a 2,00 dal filo ovest)	1,60	16
Nicchia esterna, larga × profonda	1,30 × 0,85	13 × 8,5
Bocca verso la corte, larga × profonda	1,00 × 0,55	10 × 5,5
Gola tra bocca e camera, larga × lunga	0,60 × 0,15	6 × 1,5
Vano sotto il focolare, altezza	0,90	9
Soletta del focolare, spessore	0,30	3
Bocca del focolare, da / a sul pavimento	1,20 - 1,46	12 - 14,6
Canna fumaria, est-ovest × nord-sud	0,60 × 0,60	6 × 6
Canna fumaria, altezza sopra il tetto	1,85	18,5

Come leggere le quote (in metri)

nero: scritta sulla scheda del prof

blu: misurata sul disegno della scheda (margine circa 5-10 cm)


rosso: ipotesi, la scheda non la dice: da chiedere al prof

Sul plastico in scala 1:100: moltiplica per 10 e leggi millimetri (1,50 m = 15 mm).

Cucina e bagno in pianta, scala 1:25


Le misure interne, i muri, le aperture, le finestre e gli arredi leggibili sulla scheda. Nord in alto, ovest a sinistra.

Cucina

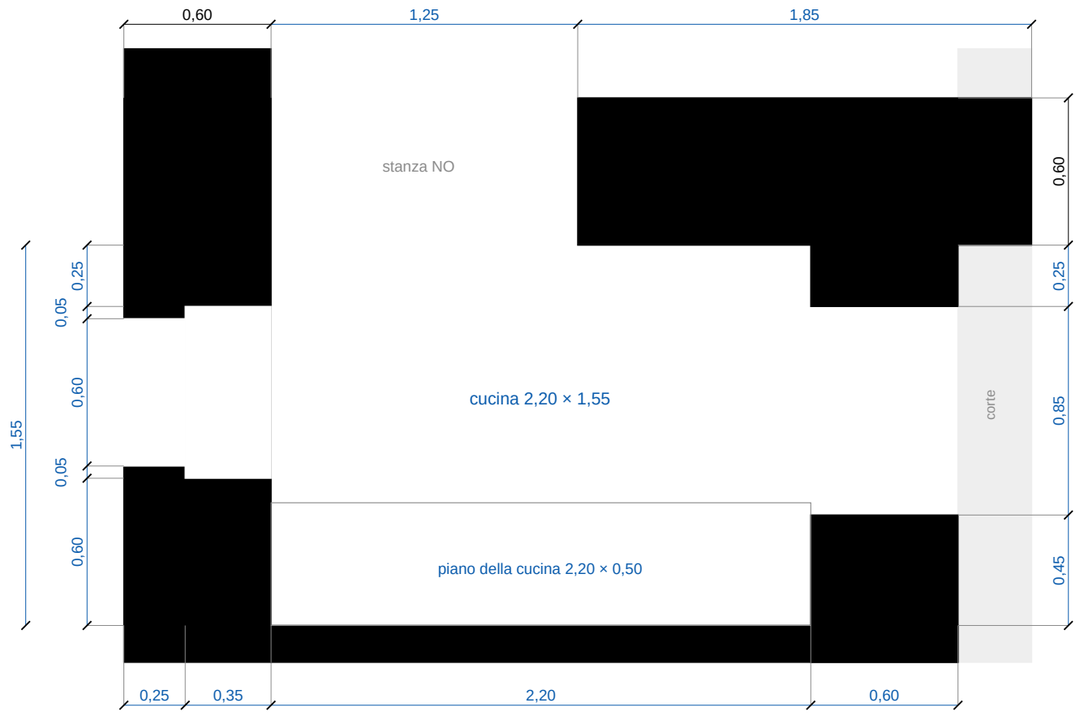

Cucina: cosa	Metri	Plastico (mm)
Interno, est-ovest × nord-sud	2,20 × 1,55	22 × 15,5
Altezza dei muri sul pavimento	3,30	33
Passaggio verso la stanza NO, senza muro né porta	1,25	12,5
Muro verso la stanza NO, lungo × spesso	1,85 × 0,60	18,5 × 6
Muro verso la corte, spessore	0,60	6
Apertura sulla corte, larga	0,85	8,5
Apertura sulla corte, altezza	2,10	21
Muro tra stanza NO e apertura	0,25	2,5
Finestra ovest, larga fuori / dentro	0,60 / 0,70	6 / 7
Finestra ovest, da / a sul pavimento	1,05 - 1,70	10,5 - 17
Piano della cucina, altezza: la scheda non la dà	-	-

Bagno

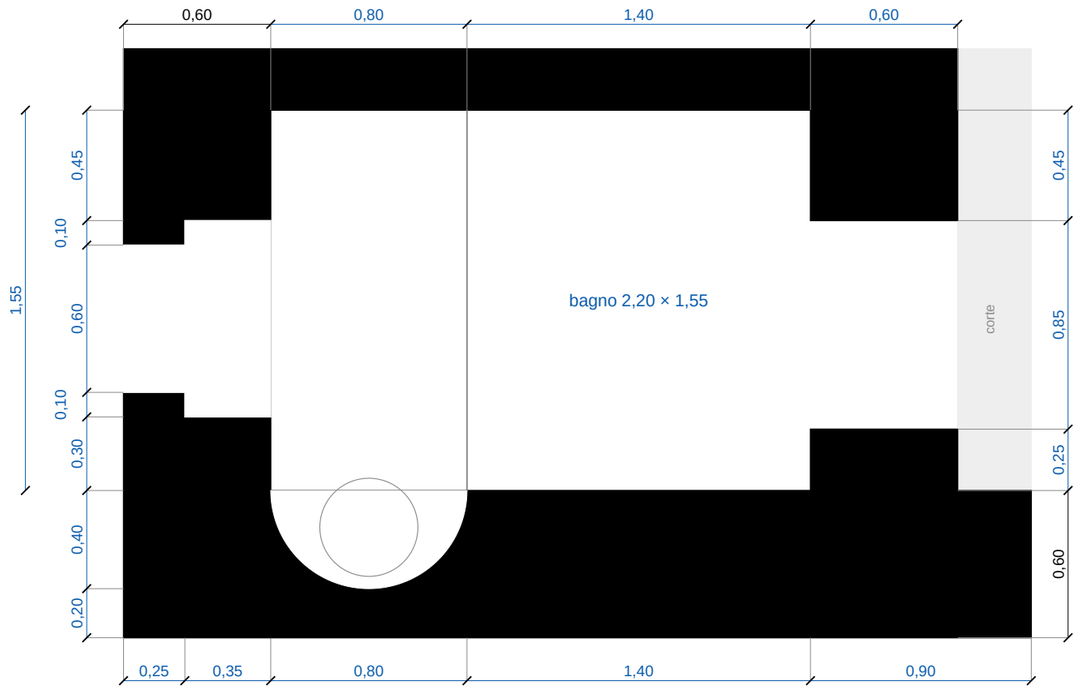

Bagno: cosa	Metri	Plastico (mm)
Interno, est-ovest × nord-sud	2,20 × 1,55	22 × 15,5
Altezza dei muri sul pavimento	3,30	33
Tramezzo sottile a 0,80 dal muro ovest	0,80 + 1,40	8 + 14
Nicchia a sud, larga × profonda	0,80 × 0,40	8 × 4
Elemento rotondo nella nicchia, diametro	0,40	4
Muro verso il camino: massa del blocco	vedi tavola 2	
Muro verso la stanza SO, spessore	0,60	6
Apertura sulla corte, larga	0,85	8,5
Apertura sulla corte, altezza	2,10	21
Finestra ovest, larga fuori / dentro	0,60 / 0,80	6 / 8
Finestra ovest, da / a sul pavimento	1,05 - 1,70	10,5 - 17

Le linee sottili degli arredi sulla scheda sono sfocate: il tramezzo e il cerchio sono quello che si riesce a leggere. Sul plastico chiuso non si vedono e puoi non farli.

Come leggere le quote (in metri)

nero: scritta sulla scheda del prof
blu: misurata sul disegno della scheda (margine circa 5-10 cm)
rosso: ipotesi, la scheda non la dice: da chiedere al prof
Sul plastico in scala 1:100: moltiplica per 10 e leggi millimetri (1,50 m = 15 mm).

Camino in sezione CC', scala 1:30

Taglio lungo l'asse della casa, guardando verso sud (ovest a destra). Quote in metri, pavimento = 0,00.


Il camino, da sotto in su

Parte	Quota	X da ovest
Vano sotto	0,00 - 0,90	1,20 - 3,40
Soletta	0,90 - 1,20	0,85 - 3,40
Bocca del focolare	1,20 - 1,46	2,80 - 3,40
Cupola del focolare	1,20 - 1,62	1,52 - 2,80
Massa piena	fino a 3,20	1,20 - 3,12
Muro di fondo	fino a 3,30	0,85 - 1,20
Canna fumaria	3,30 - 5,15	2,80 - 3,40

Le due canne, dalla corte verso ovest: parete 0,08, canna aperta in cima 0,11 (scende fino al focolare), setto 0,09, vuoto chiuso 0,24, parete 0,08; cappello alto 0,11 sopra setto e vuoto.

La canna è alta 1,85 sopra il tetto: 1,80 in questa sezione, 1,92 nella facciata BB'. Ho preso la media. Sul plastico 18-19 mm vanno bene.

Le canne e la cupola stanno dentro il blocco: sul plastico chiuso non si vedono. Da fuori si vedono il blocco, la canna e la bocca verso la corte.

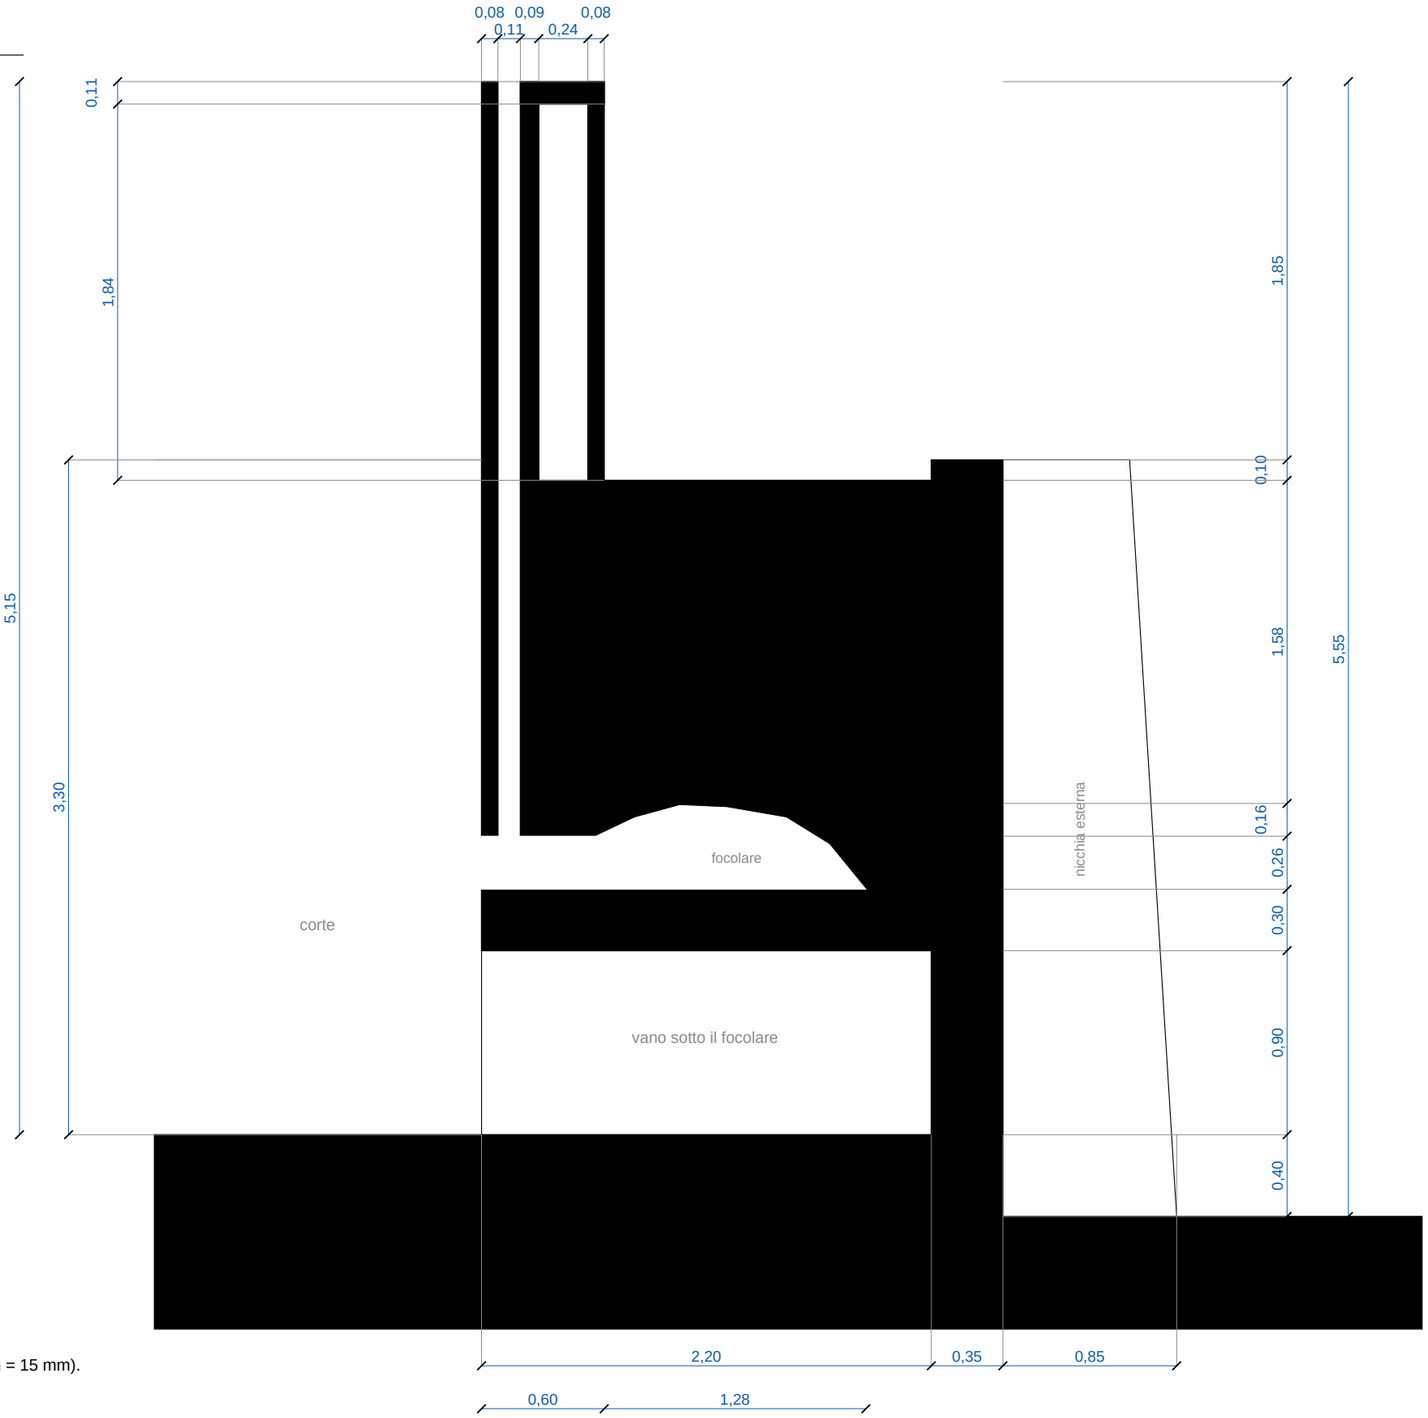


Come leggere le quote (in metri)


nero: scritta sulla scheda del prof
blu: misurata sul disegno della scheda (margine circa 5-10 cm)
rosso: ipotesi, la scheda non la dice: da chiedere al prof
Sul plastico in scala 1:100: moltiplica per 10 e leggi millimetri (1,50 m = 15 mm).

Sezione AA', scala 1:50

Taglio nord-sud lungo l'asse della casa, guardando verso est (nord a sinistra). Quote in metri, pavimento = 0,00.

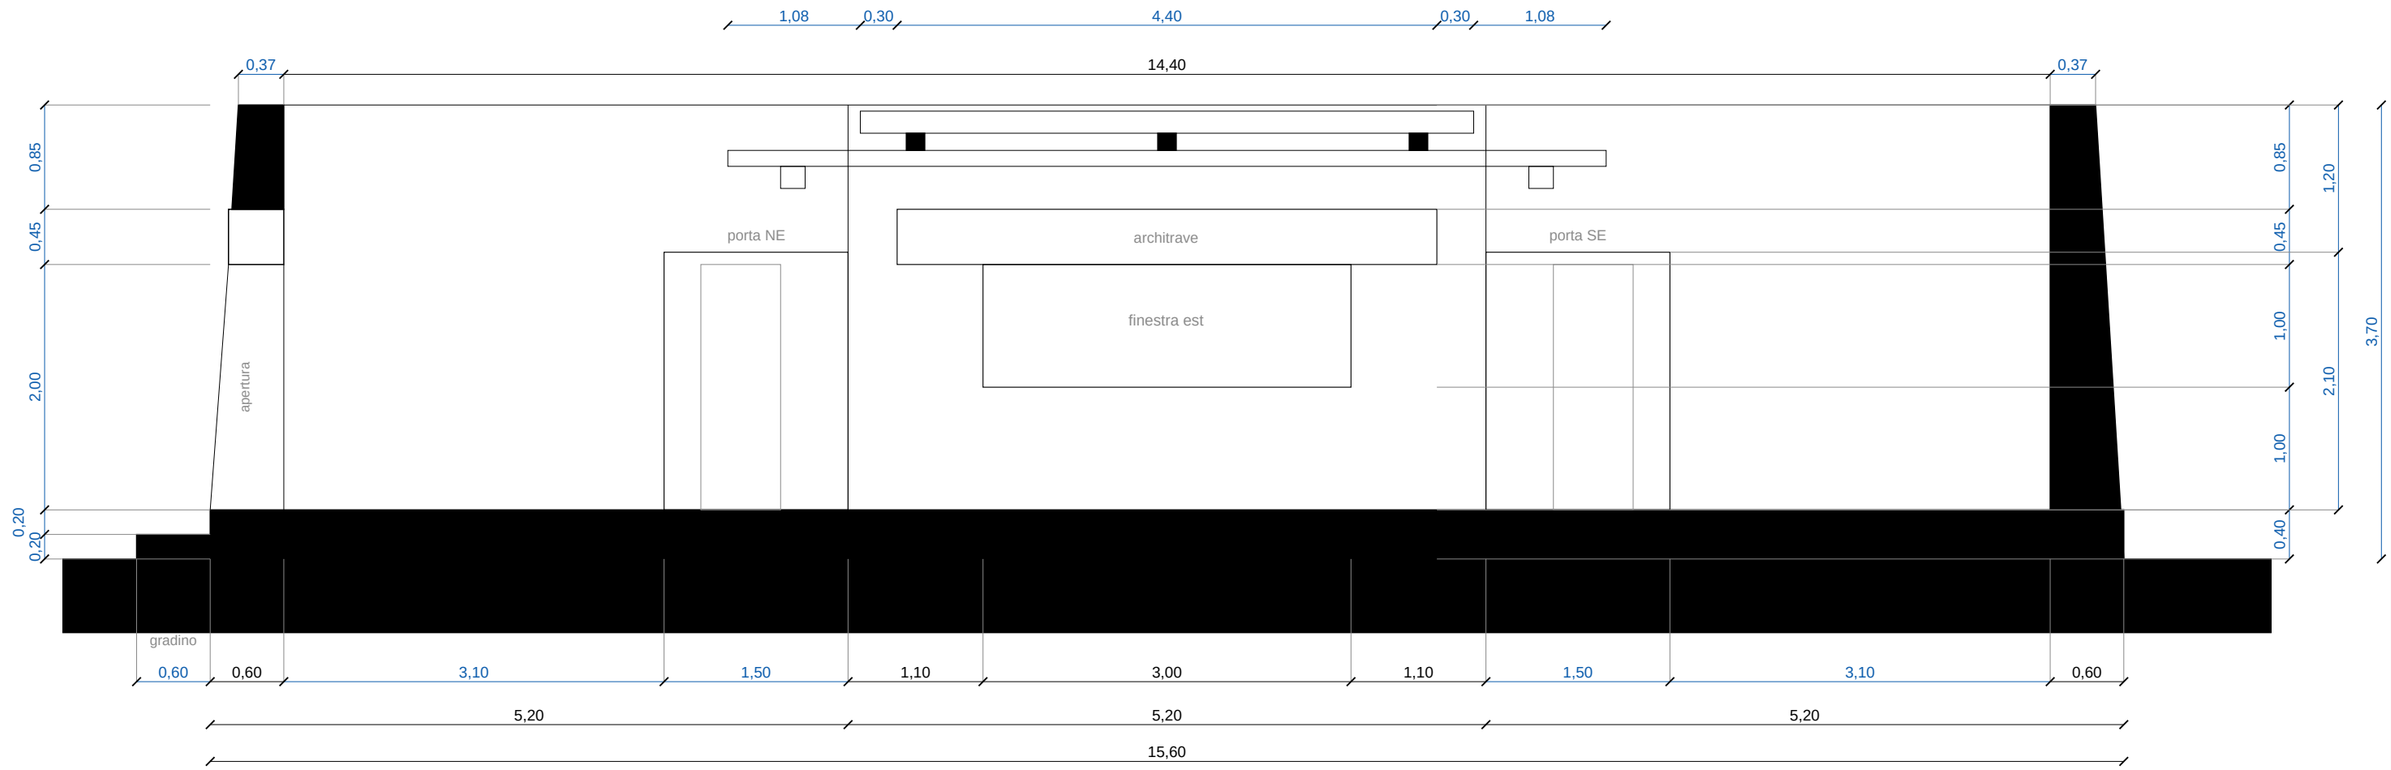

Dettaglio della copertura leggera, 1:25 (lato nord, il lato sud è uguale e simmetrico rispetto a Y = 7,80)

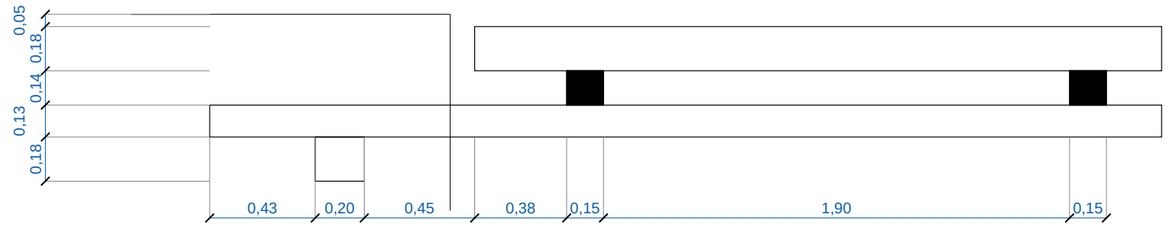

Dall'alto in basso: telo di canne (spessore 0,18), travi est-ovest nere (0,15 × 0,14, passo 2,05), travi nord-sud (spessore 0,13), mensole sotto le travi nord-sud (0,20 × 0,18).

In pianta il telo è 7,00 (est-ovest) × 5,00 (nord-sud).
Le travi nord-sud sono lunghe 7,15; distano 4,90 (X = 5,35 e 10,25).

Queste quote possono variare di 5-7 cm: AA' e CC' non coincidono perfettamente. Sul plastico basta un cartoncino a quota 3,10.

Come leggere le quote (in metri)


nero: scritta sulla scheda del prof
blu: misurata sul disegno della scheda (margine circa 5-10 cm)
rosso: ipotesi, la scheda non la dice: da chiedere al prof
Sul plastico in scala 1:100: moltiplica per 10 e leggi millimetri (1,50 m = 15 mm).

Spessore del tetto delle stanze: la scheda non lo mostra.
Sul plastico usa lo spessore del materiale, a filo del muro in cima.

Il terreno sotto la linea di taglio è solo grafico, non è una misura.

Sezione CC', scala 1:50

Taglio est-ovest lungo l'asse della casa, guardando verso sud (est a sinistra, ovest a destra). Quote in metri, pavimento = 0,00.

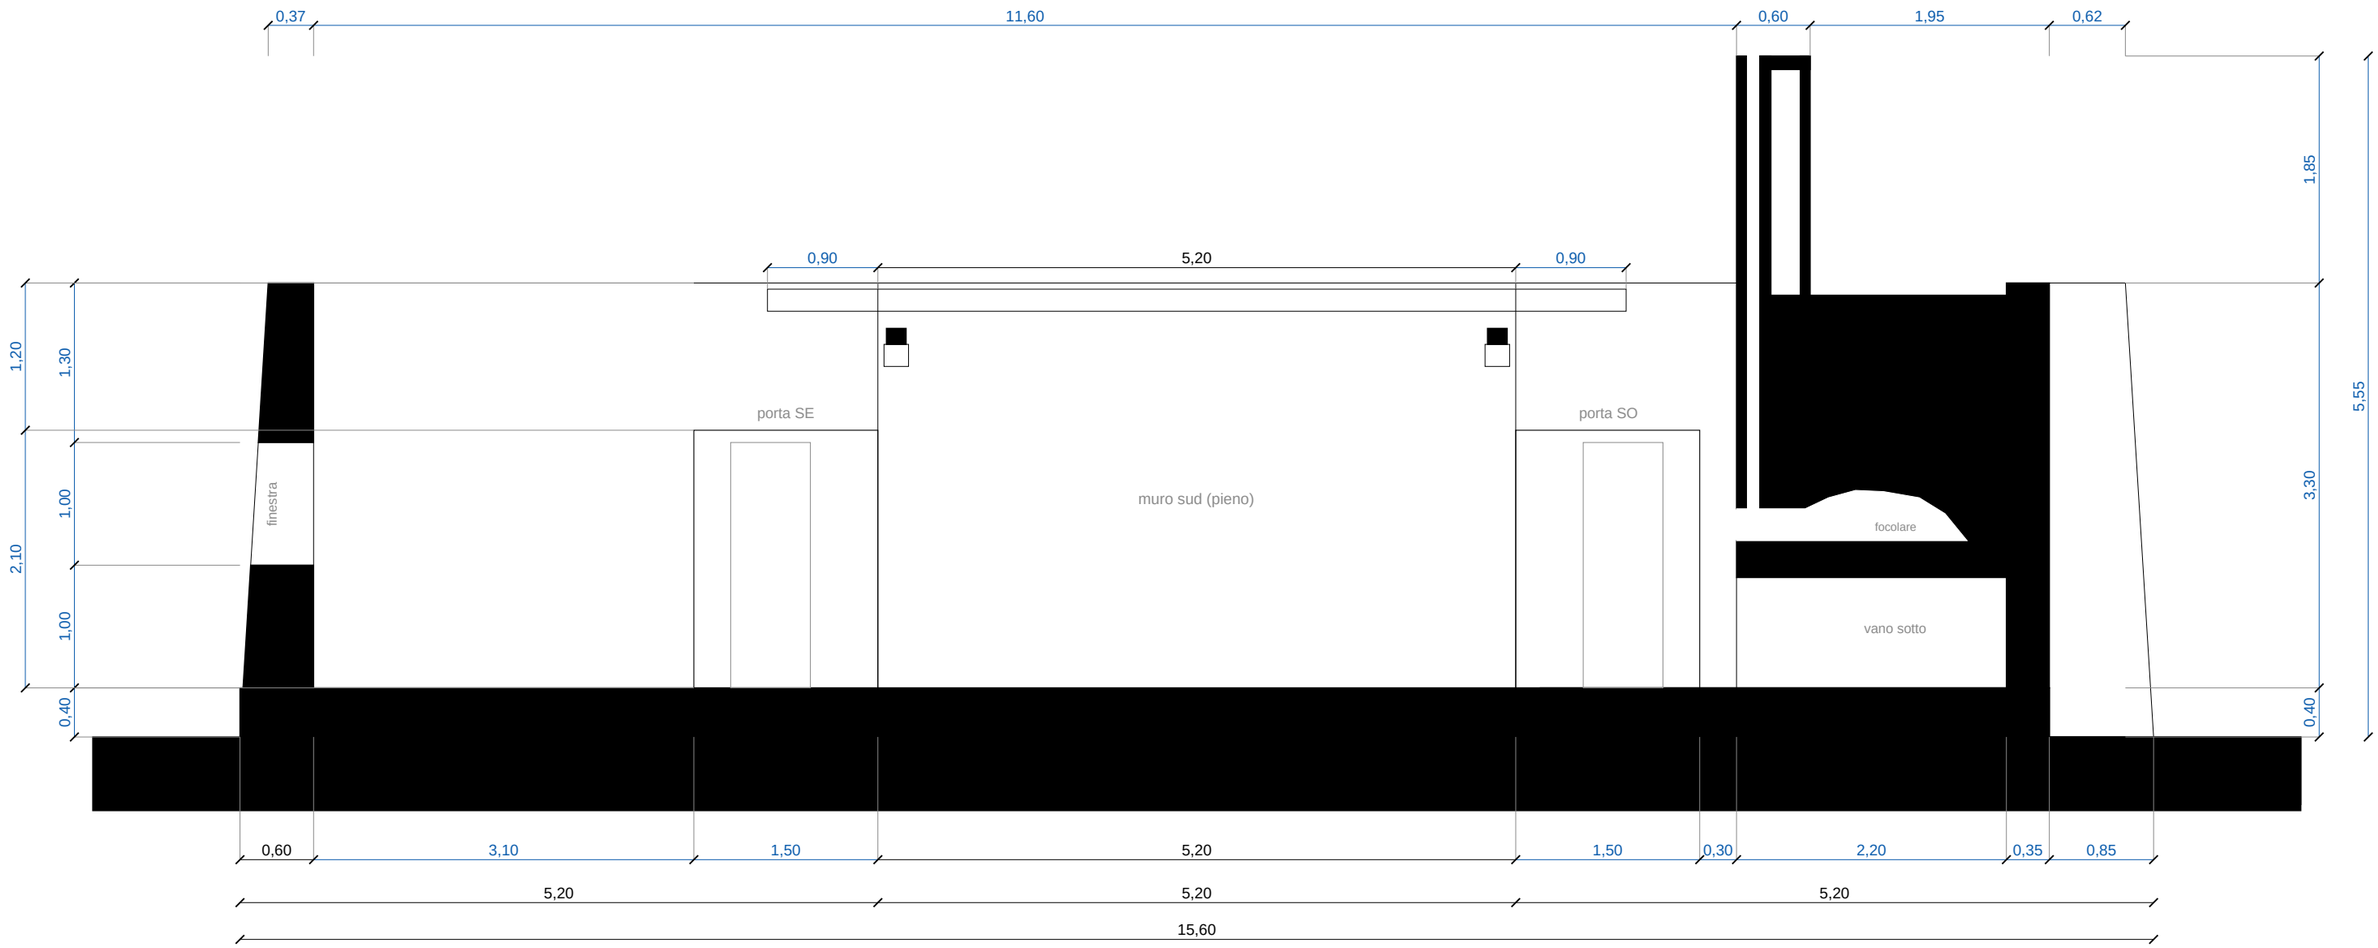

Il camino è disegnato con tutte le sue misure nella tavola 4.


Il muro esterno è inclinato: 0,60 a terra, 0,37 in cima. Sul plastico puoi farlo dritto (5-6 mm) e tenere l'altezza totale di 37 mm dal terreno.

Come leggere le quote (in metri)

nero: scritta sulla scheda del prof
blu: misurata sul disegno della scheda (margine circa 5-10 cm)
rosso: ipotesi, la scheda non la dice: da chiedere al prof
Sul plastico in scala 1:100: moltiplica per 10 e leggi millimetri (1,50 m = 15 mm).

Sezione BB' (facciata nord), scala 1:50

Vista da fuori, guardando verso sud (est a sinistra, ovest a destra). Quote in metri, terreno = -0,40, pavimento = 0,00.

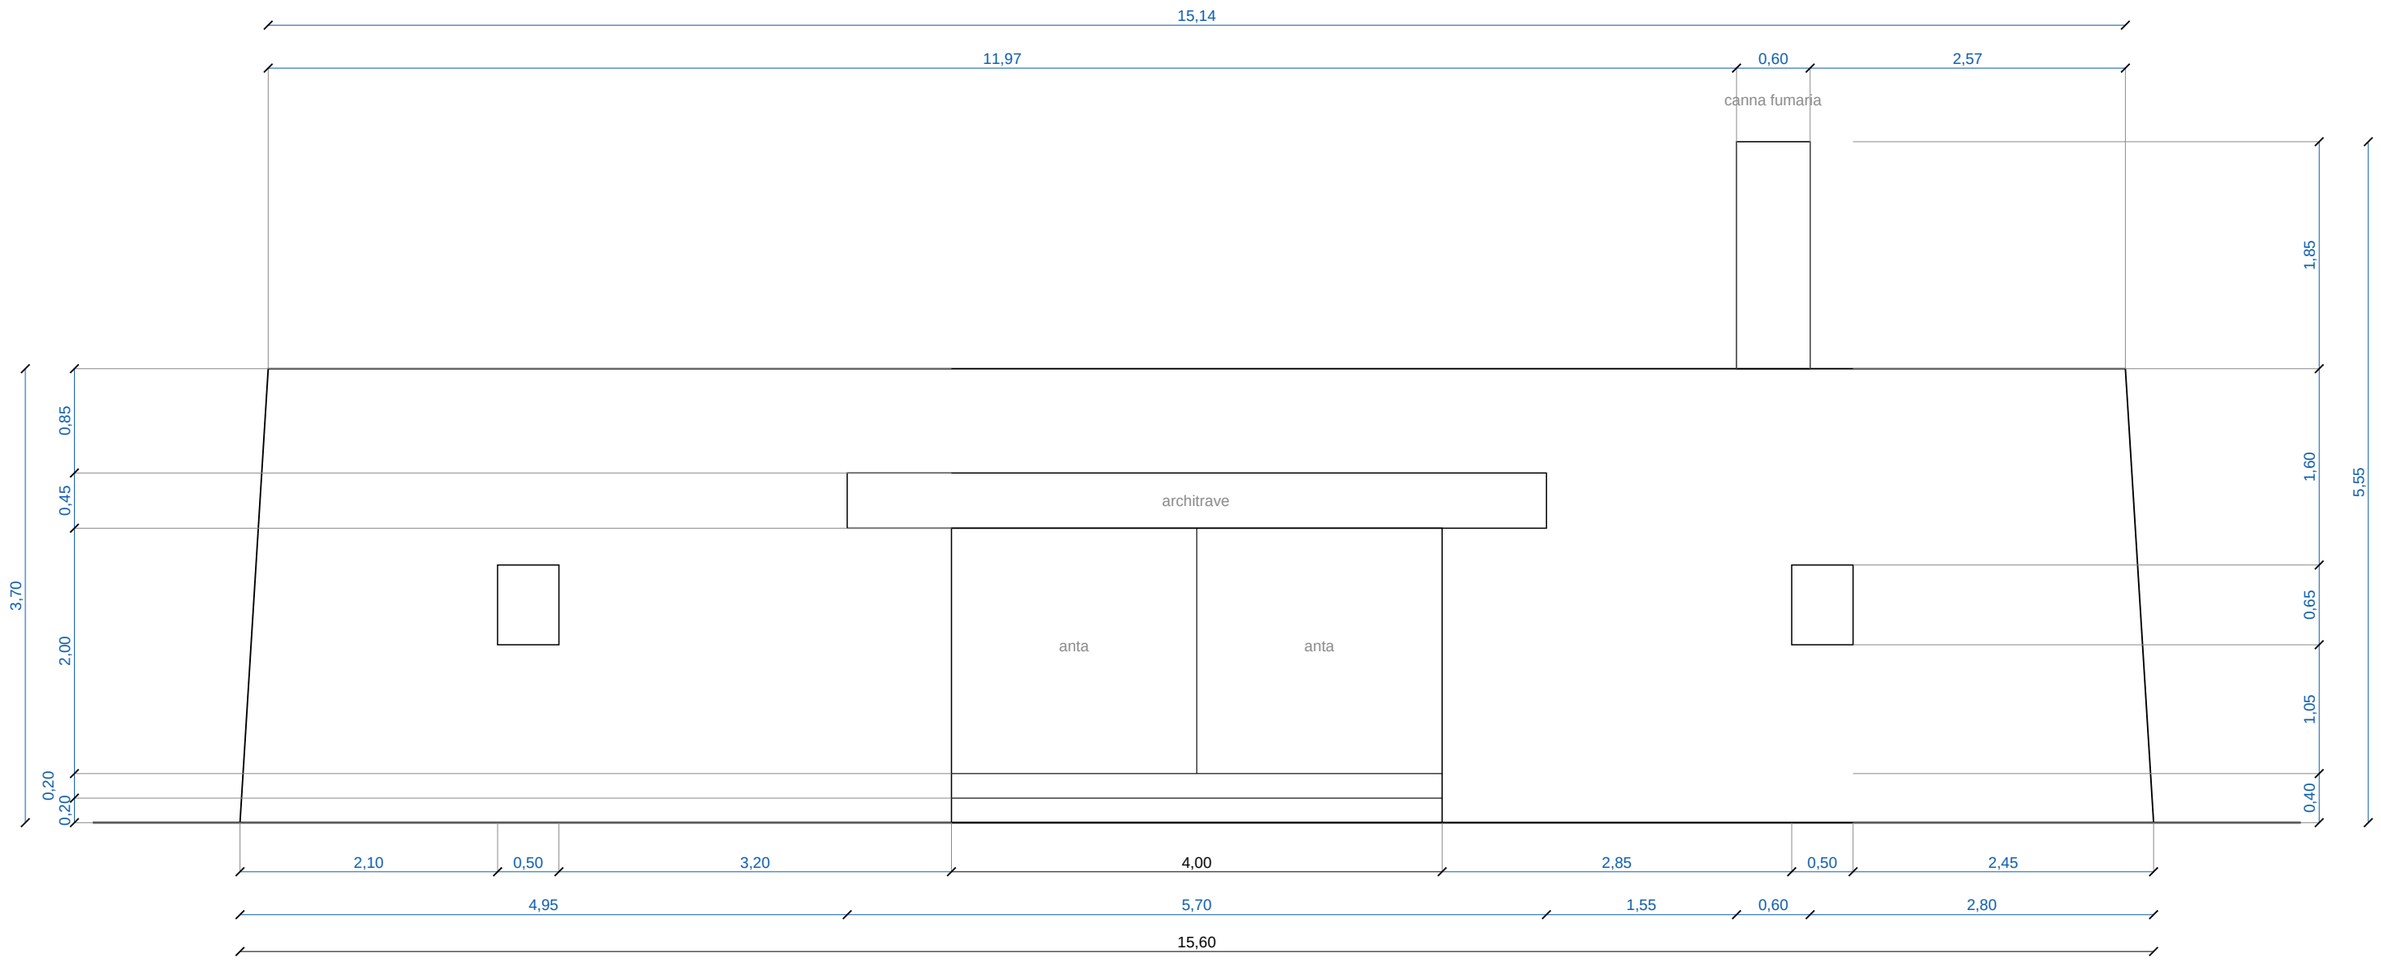

L'apertura nord è larga 4,00 e ha due ante da 2,00, alte fino a 2,00 sul pavimento.

Due gradini (0,20 ciascuno) portano dal terreno al pavimento; il gradino basso è profondo 0,60.

L'architrave di 5,70 sporge 0,85 per parte oltre l'apertura.

Come leggere le quote (in metri)

nero: scritta sulla scheda del prof

blu: misurata sul disegno della scheda (margine circa 5-10 cm)

rosso: ipotesi, la scheda non la dice: da chiedere al prof

Sul plastico in scala 1:100: moltiplica per 10 e leggi millimetri (1,50 m = 15 mm).