Nuova disposizione: pianta quotata, scala 1:100

Stessi ambienti e stesso perimetro della casa di Zanuso. Stampa in A3 al 100% e il lato della casa misura 156 mm.



Le quattro porte delle stanze (X da ovest, Y da nord)

Porta	Muro che si interrompe	Altro muro	Larghezza
In alto al centro	sud a X = 8,90	est a Y = 3,70	1,27
In alto a destra	sud a X = 11,90	ovest a Y = 3,70	1,27
Sul lato est	nord a X = 11,90	ovest a Y = 6,70	1,27
In basso a sinistra	nord a X = 3,70	est a Y = 11,90	1,27

Le sei finestre

Finestra	Posizione	Larg.	Da / a sul pav.
Bagno, muro nord	X da 1,10 a 1,70	0,60	1,05 - 1,70
Cucina, muro nord	X da 3,55 a 4,15	0,60	1,05 - 1,70
Stanza in alto al centro, nord	X da 7,55 a 8,05	0,50	1,05 - 1,70
Stanza in alto a destra, nord	X da 13,00 a 13,50	0,50	1,05 - 1,70
Stanza sul lato est, est	Y da 7,55 a 8,05	0,50	1,05 - 1,70
Stanza in basso a sin., ovest	Y da 13,00 a 13,60	0,60	1,05 - 1,70

Altezze e ingresso

Altezze	Metri	Plastico (mm)
Muri, sul pavimento	3,30	33
Rialzo della casa sul terreno	0,40	4
Porte delle stanze	2,10	21
Ingresso a sud, larghezza × altezza	4,00 × 2,00	40 × 20
Architrave dell'ingresso, lungo × alto	5,70 × 0,45	57 × 4,5
Due gradini fuori dall'ingresso, alti e profondi	0,20 e 0,30	2 e 3

Come leggere le quote (in metri)

nero: misura della casa vera

blu: posizione presa dal tuo schizzo

rosso: scelta mia, nello schizzo non c'è: puoi cambiarla

Sul plastico in scala 1:100: moltiplica per 10 e leggi millimetri (1,50 m = 15 mm).


Tratteggio esterno: filo del muro in cima (i muri esterni sono inclinati). Grigio: vuoto scoperto. Tratteggio rosso sul camino: canna fumaria.

I muri tra stanze vicine sono doppi (0,60 + 0,60 = 1,20), perché ogni stanza tiene i suoi muri come nella griglia di Zanuso.

Nuova disposizione: i dettagli

Ingresso comune delle tre stanze 1:25, bagno e cucina 1:50, camino 1:50.

Ingresso comune delle tre stanze, 1:25

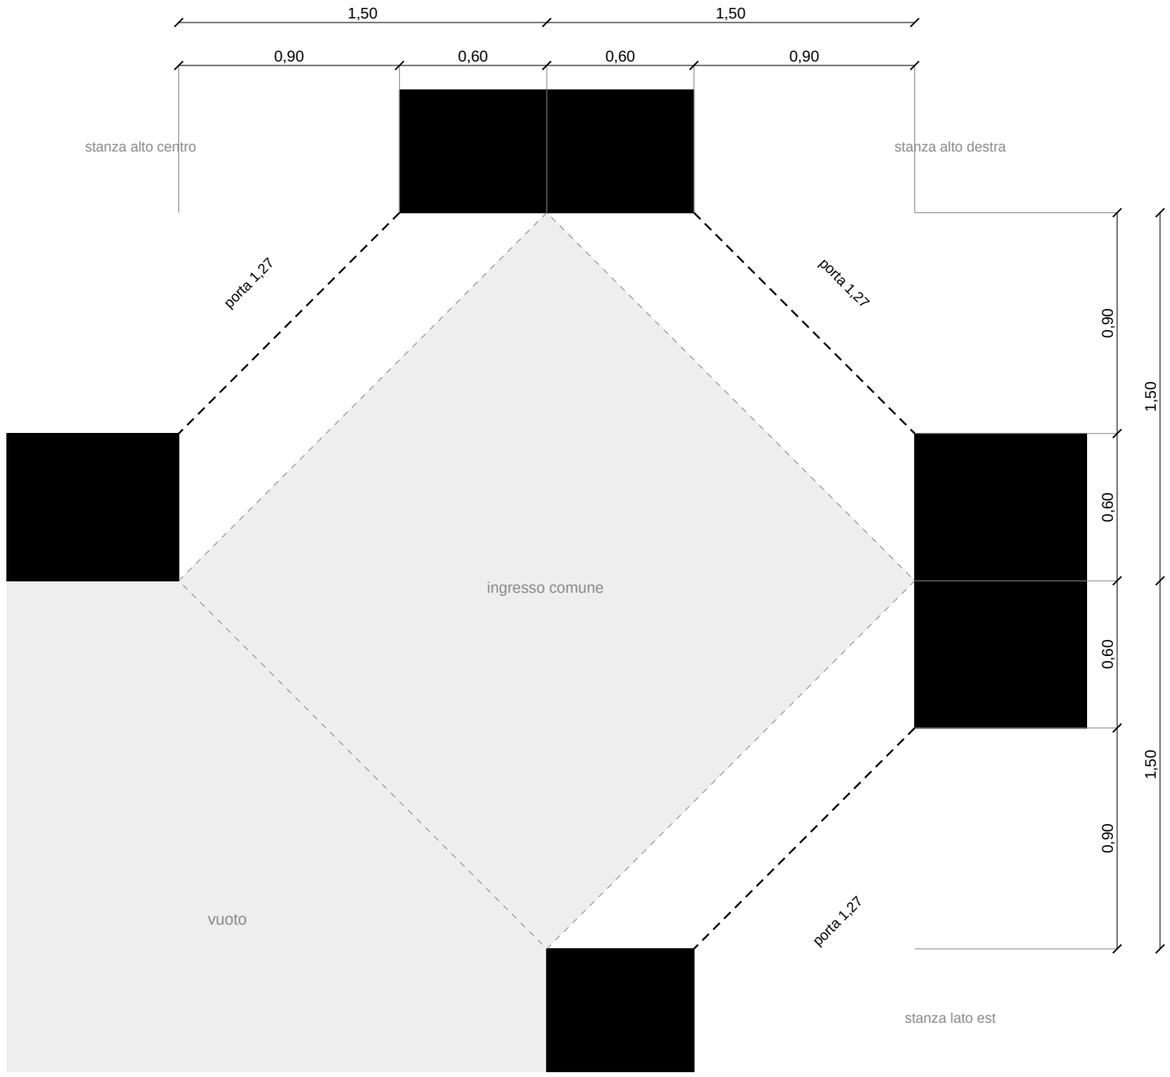


Ogni muro si ferma a 1,50 m dall'angolo in cui si incontrano le tre stanze, come nella casa vera. L'angolo sta a X = 10,40 e Y = 5,20: sul plastico a 104 mm dal bordo ovest e 52 mm dal bordo nord. Le porte sono alte 2,10 m: sopra, i muri continuano fino all'angolo, quindi l'ingresso comune resta coperto.


Come leggere le quote (in metri)

nero: misura della casa vera
blu: posizione presa dal tuo schizzo
rosso: scelta mia, nello schizzo non c'è: puoi cambiarla
Sul plastico in scala 1:100: moltiplica per 10 e leggi millimetri (1,50 m = 15 mm).

Bagno e cucina, 1:50

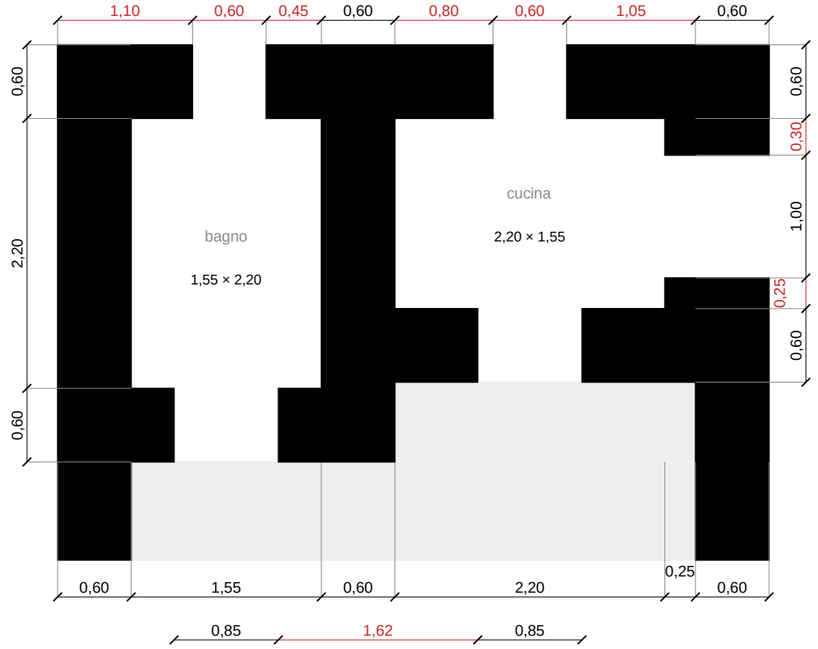

Camino, 1:50 (come quello vero, ribaltato sul muro est)

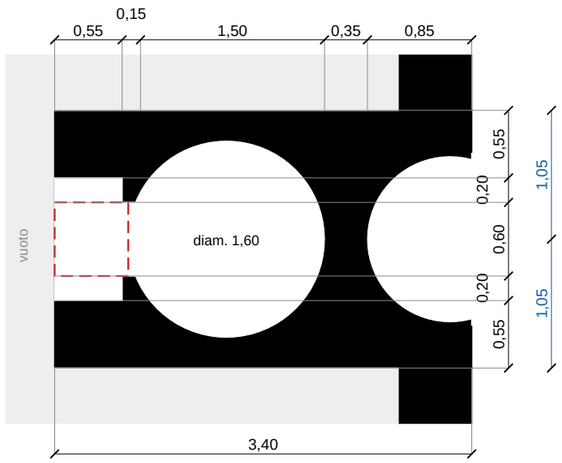

Camino	Metri	mm
Blocco largo	2,10	21
Sporge dal bordo est	3,40	34
Altezza blocco	3,20	32
Bocca, larga	1,00	10
Canna fumaria	0,60 × 0,60	6 × 6
Sopra il tetto	1,85	18,5

La bocca guarda a ovest, verso l'ingresso. Il blocco è centrato sul suo quadrato, a 13,00 m dal bordo nord (130 mm).
Le altezze del camino sono nella tavola 4 della casa vera.
Bagno e cucina hanno le misure della casa vera. Nel tuo schizzo il bagno era più profondo: con le misure vere davanti resta una striscia di vuoto. Il muro est della cucina è spesso 0,85: sul plastico bastano 2 strati di Poliplat.
Il passaggio tra cucina e stanza è largo 1,00, con altezza 2,10 (scelta mia).