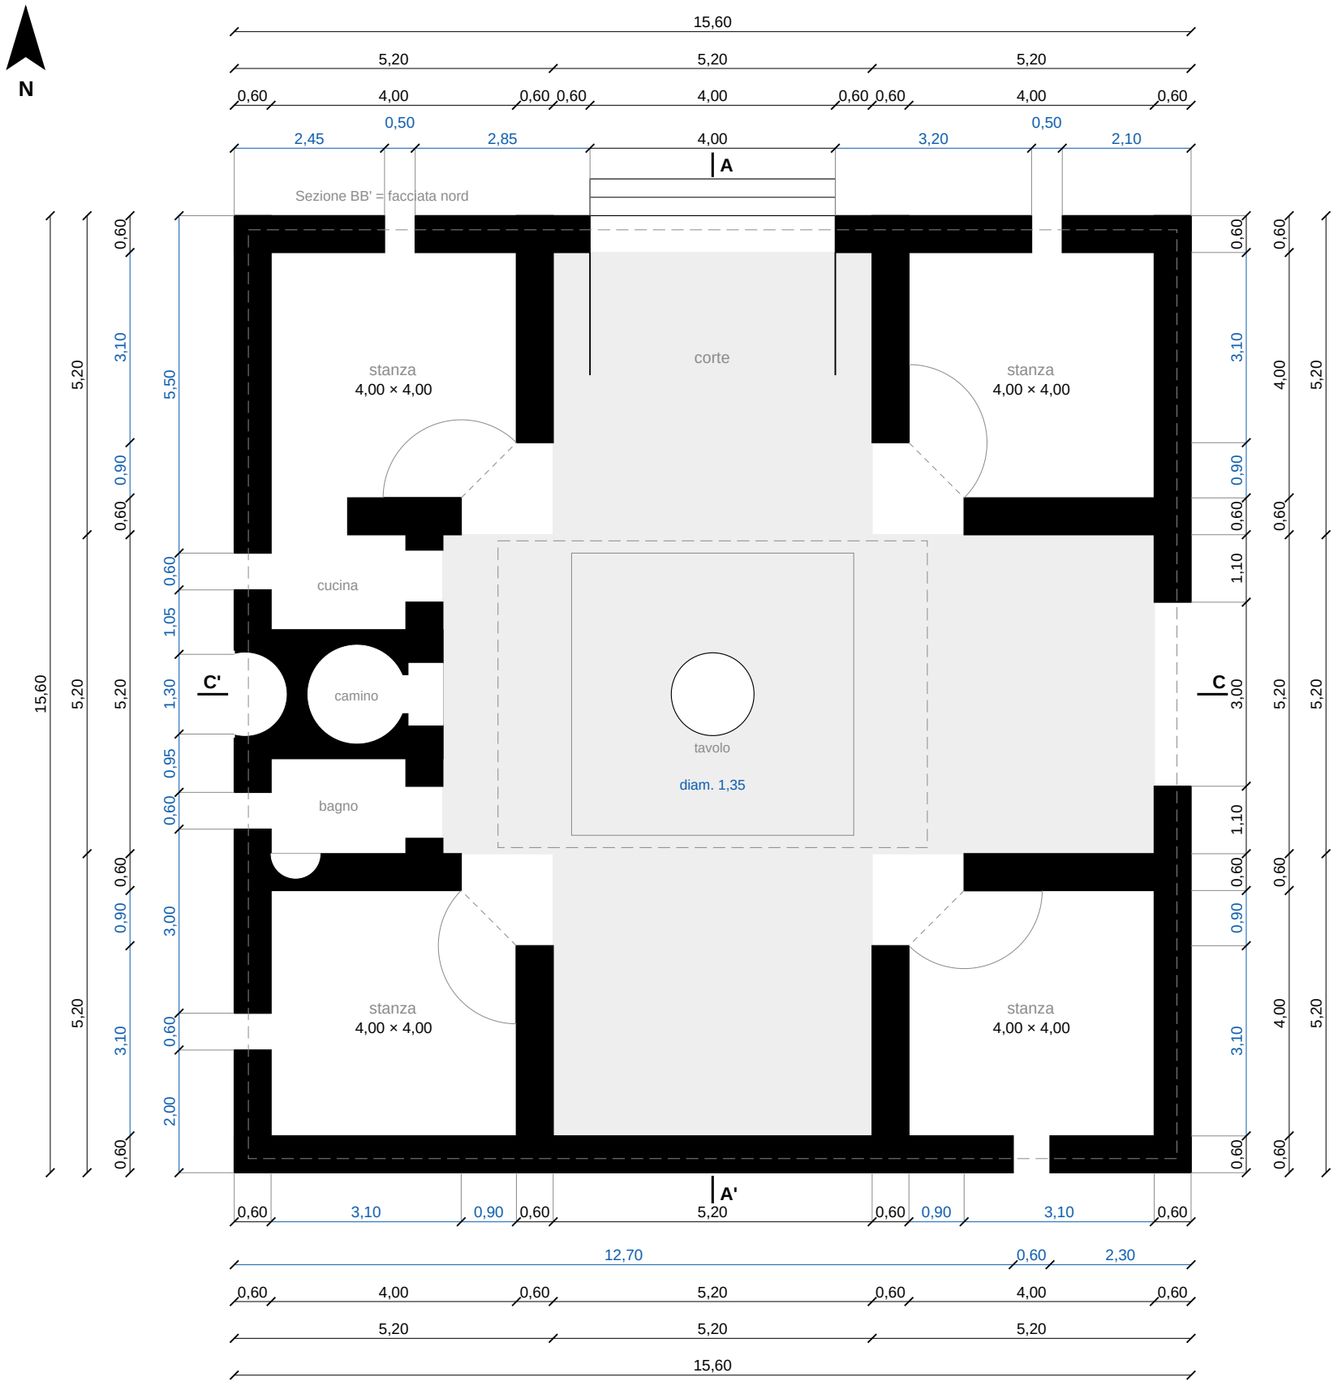
Pianta quotata, scala 1:100


Pianta tagliata all'altezza delle finestre. Stampa in A3 al 100% e il lato della casa misura 156 mm.


N
15,60
5,20
5,20
5,20
0,60
4,00
0,60
0,60
4,00
0,60
0,60
4,00
0,60
0,50
0,50
2,45
2,85
4,00
3,20
2,10
A
Sezione BB' = facciata nord
stanza
4,00 × 4,00
corte
stanza
4,00 × 4,00
cucina
camino
C'
C
bagno
tavolo
diam. 1,35
stanza
4,00 × 4,00
stanza
4,00 × 4,00
A'
15,60
5,20
5,20
5,20
5,50
3,00
2,00
1,30
0,95
1,05
0,60
3,10
0,90
1,10
4,00
3,00
0,60
0,90
3,10
0,60
0,60
0,60

Fascia ovest e camino, scale 1:50 e 1:25

Cucina, massa del camino, bagno: tutte le misure.

Pianta della fascia ovest, 1:50

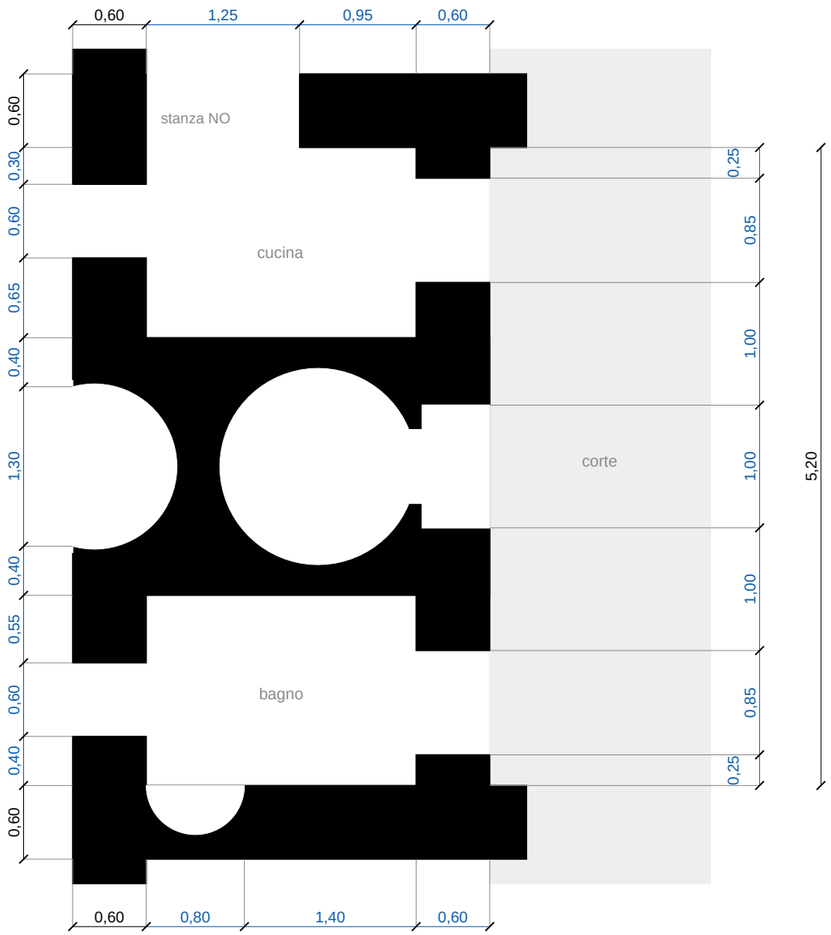


Aperture sulla corte: cucina 0,85; camino 1,00; bagno 0,85.

Altezza di cucina e bagno: 2,10 (ipotesi, come le porte).

Nicchia nel bagno: larga 0,80, profonda 0,40.

Camino in pianta, 1:25

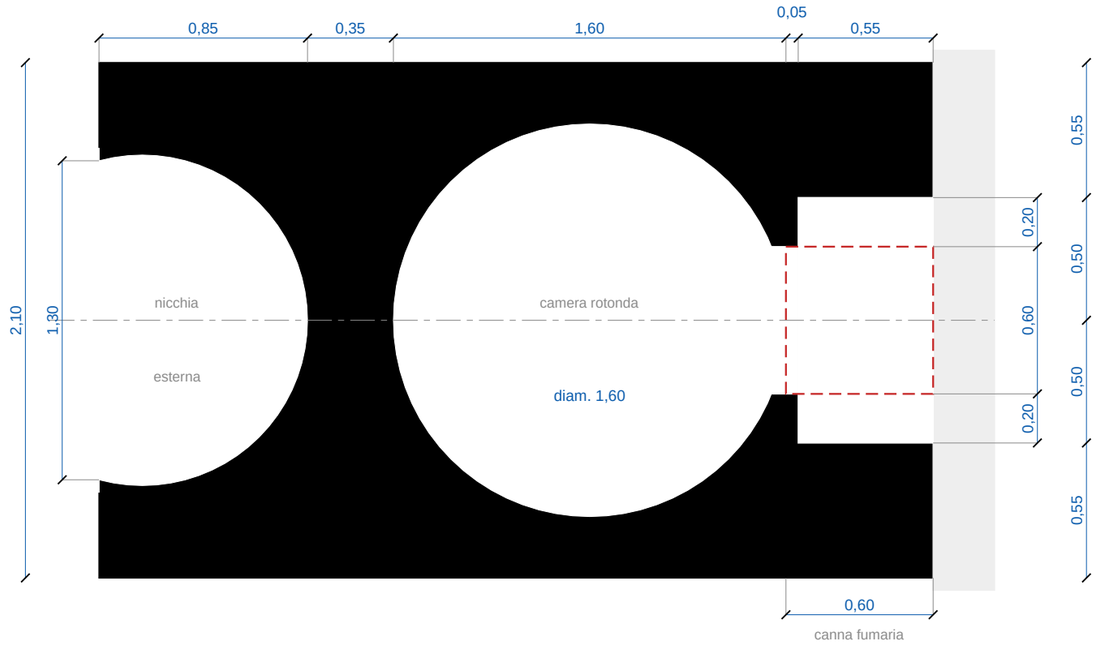

Rosso tratteggiato: canna fumaria in pianta. La scheda la mostra solo da un lato (0,60); la profondità nord-sud 0,60 è un'ipotesi: canna quadrata, centrata sull'asse del camino.

Come leggere le quote (in metri)

nero: scritta sulla scheda del prof

blu: misurata sul disegno della scheda (margine circa 5-10 cm)

rosso: ipotesi, la scheda non la dice: da chiedere al prof

Sul plastico in scala 1:100: moltiplica per 10 e leggi millimetri (1,50 m = 15 mm).

Camino in sezione CC', scala 1:30

Taglio lungo l'asse della casa, guardando verso sud (ovest a destra). Quote in metri, pavimento = 0,00.


Il camino, da sotto in su

Parte	Quota	X da ovest
Vano sotto	0,00 - 0,90	1,20 - 3,40
Soletta	0,90 - 1,20	0,85 - 3,40
Bocca del focolare	1,20 - 1,46	2,80 - 3,40
Cupola del focolare	1,20 - 1,62	1,52 - 2,80
Massa piena	fino a 3,20	1,20 - 3,12
Muro di fondo	fino a 3,30	0,85 - 1,20
Canna fumaria	3,30 - 5,15	2,80 - 3,40

Le due canne, dalla corte verso ovest: parete 0,08, canna aperta in cima 0,11 (scende fino al focolare), setto 0,09, vuoto chiuso 0,24, parete 0,08; cappello alto 0,11 sopra setto e vuoto.

La canna è alta 1,85 sopra il tetto: 1,80 in questa sezione, 1,92 nella facciata BB'. Ho preso la media. Sul plastico 18-19 mm vanno bene.

Le canne e la cupola stanno dentro il blocco: sul plastico chiuso non si vedono. Da fuori si vedono il blocco, la canna e la bocca verso la corte.

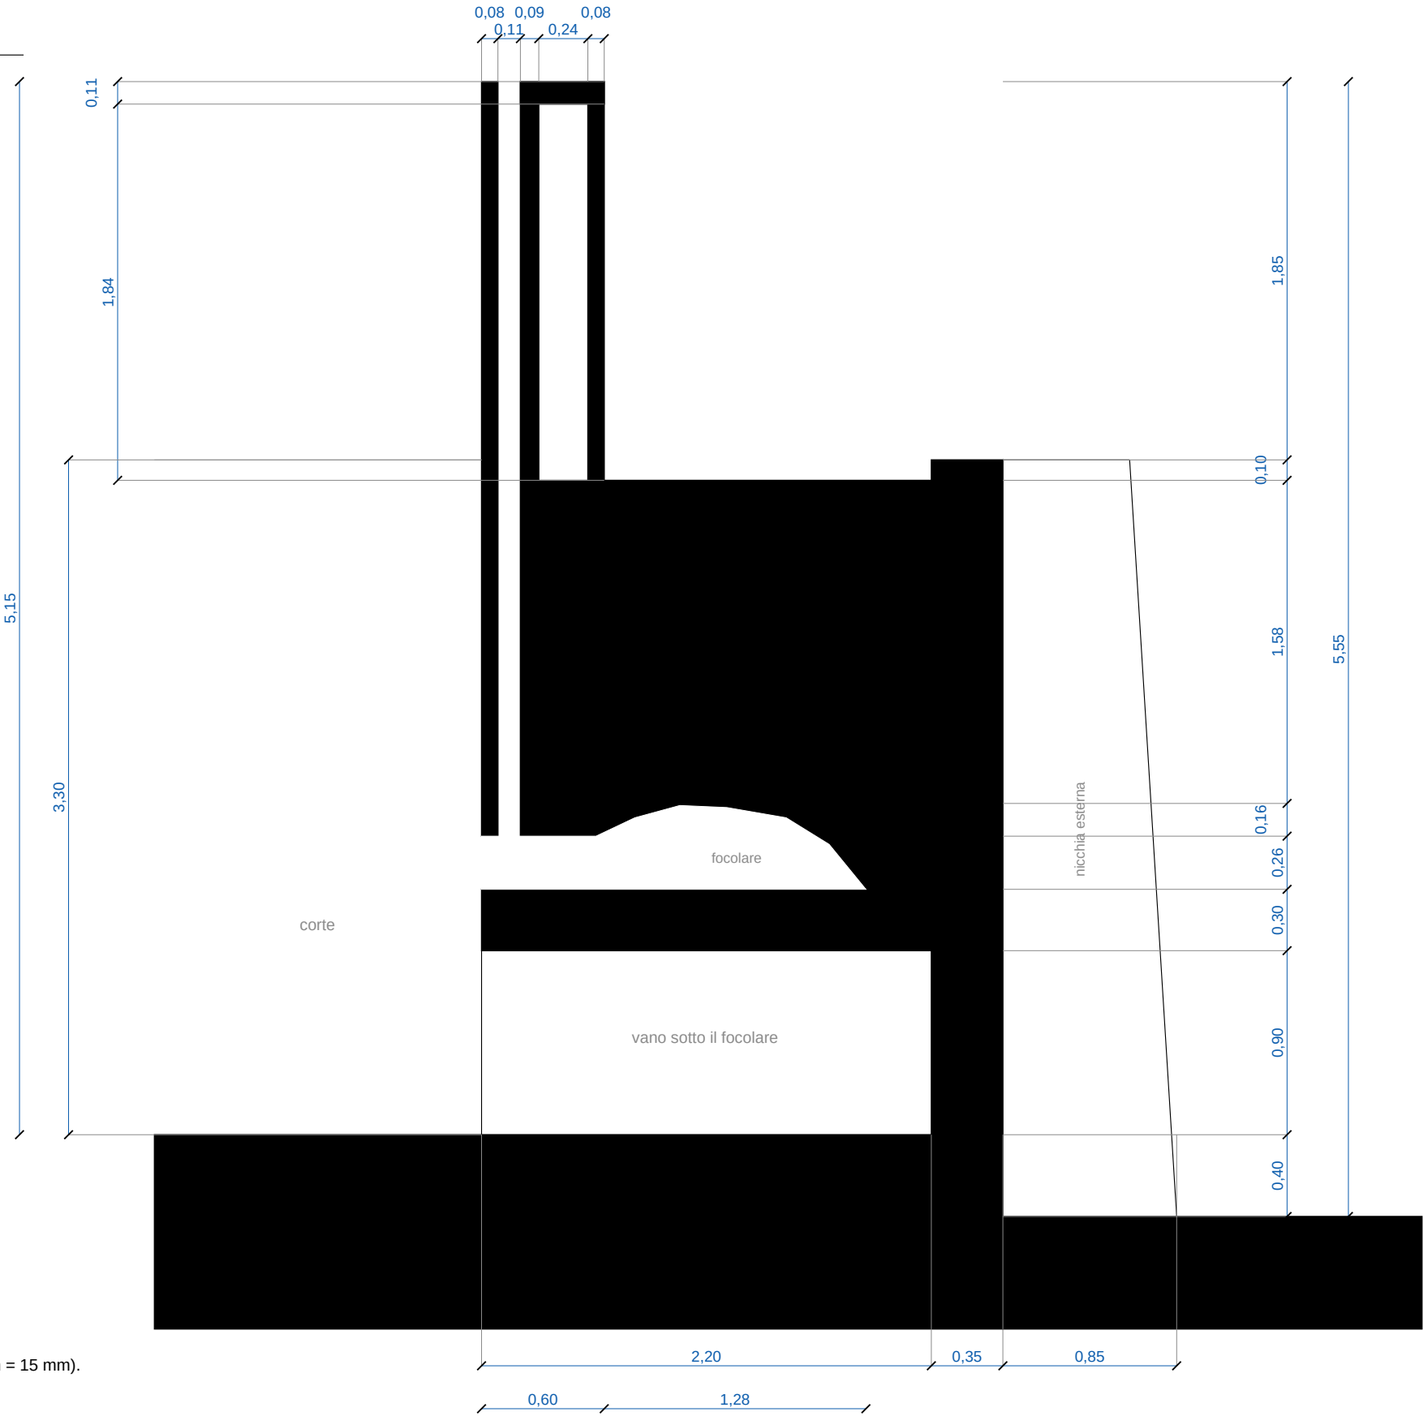


Come leggere le quote (in metri)


nero: scritta sulla scheda del prof
blu: misurata sul disegno della scheda (margine circa 5-10 cm)
rosso: ipotesi, la scheda non la dice: da chiedere al prof
Sul plastico in scala 1:100: moltiplica per 10 e leggi millimetri (1,50 m = 15 mm).

Sezione AA', scala 1:50

Taglio nord-sud lungo l'asse della casa, guardando verso est (nord a sinistra). Quote in metri, pavimento = 0,00.

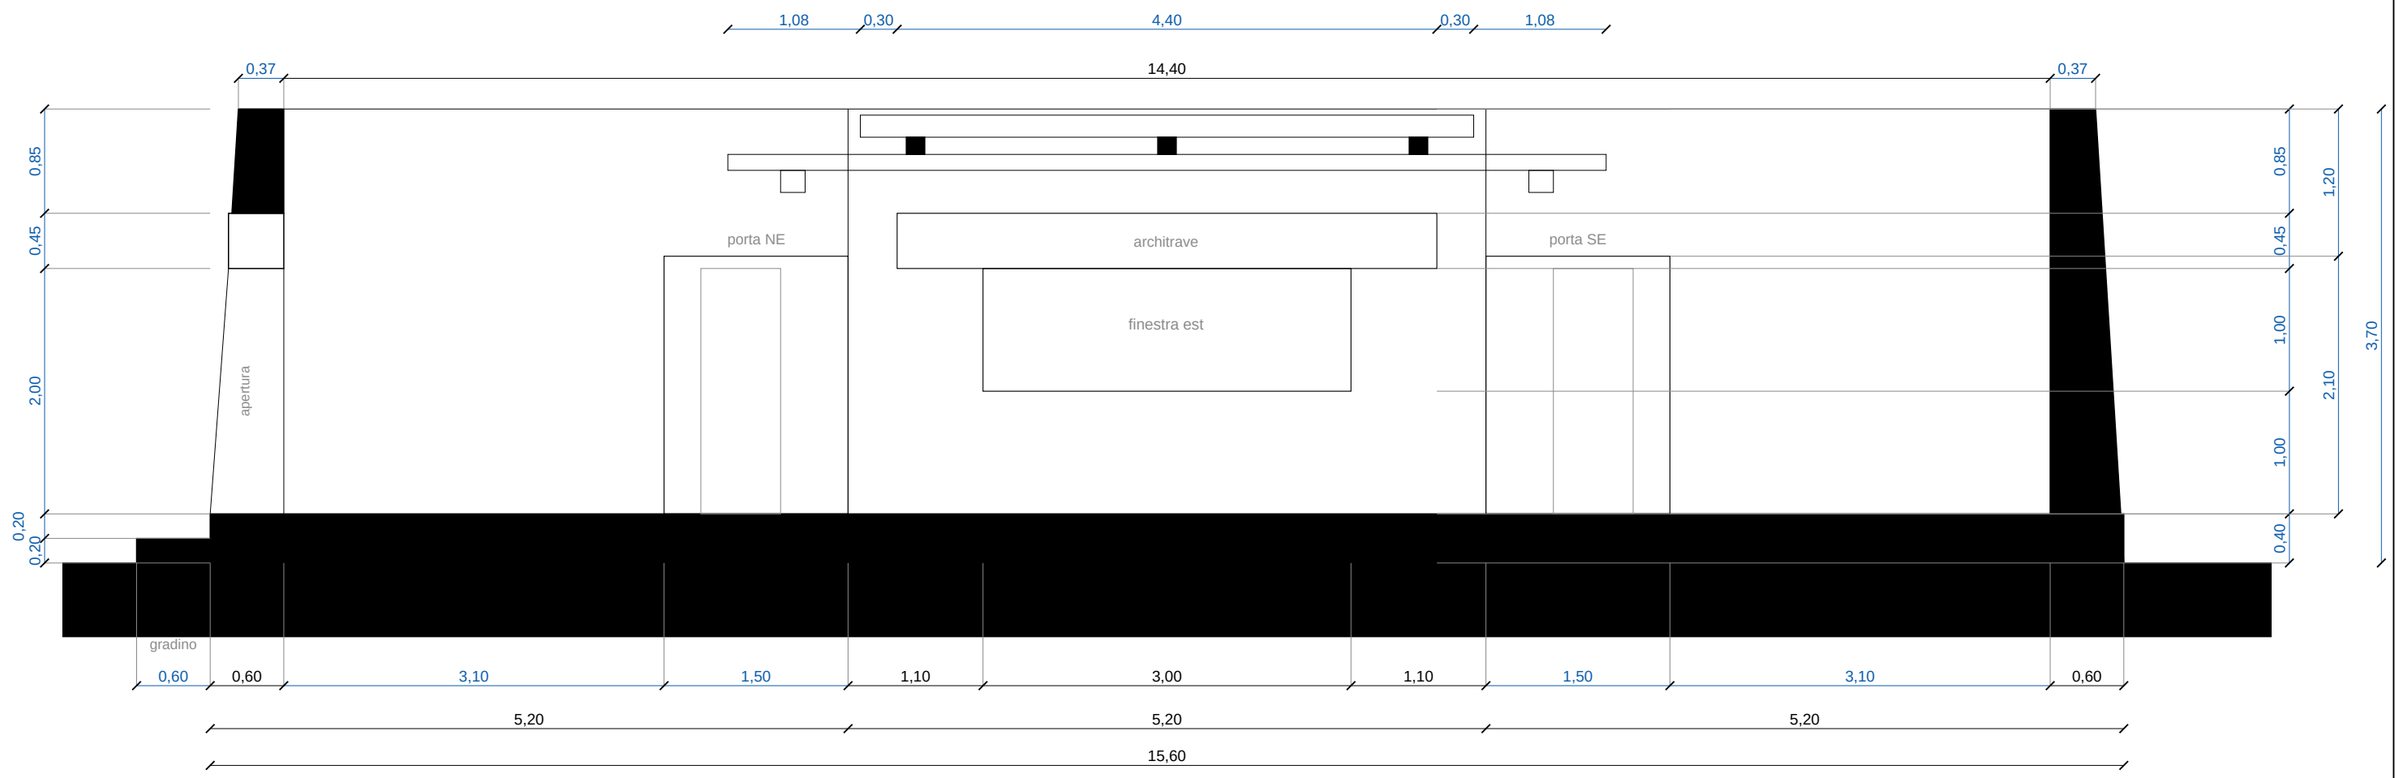

Dettaglio della copertura leggera, 1:25 (lato nord, il lato sud è uguale e simmetrico rispetto a Y = 7,80)

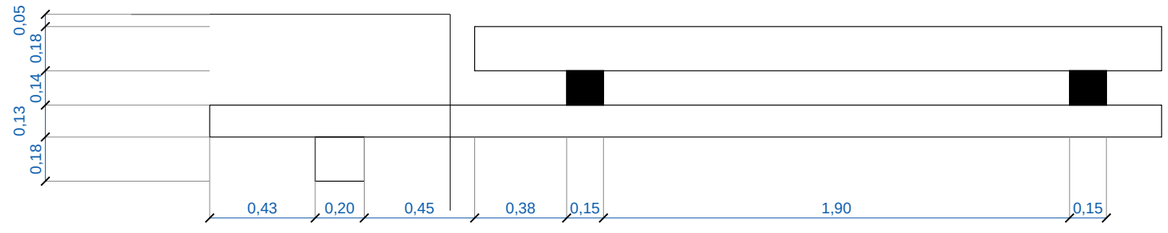

Dall'alto in basso: telo di canne (spessore 0,18), travi est-ovest nere (0,15 × 0,14, passo 2,05), travi nord-sud (spessore 0,13), mensole sotto le travi nord-sud (0,20 × 0,18).

In pianta il telo è 7,00 (est-ovest) × 5,00 (nord-sud).
Le travi nord-sud sono lunghe 7,15; distano 4,90 (X = 5,35 e 10,25).

Queste quote possono variare di 5-7 cm: AA' e CC' non coincidono perfettamente. Sul plastico basta un cartoncino a quota 3,10.

Come leggere le quote (in metri)


nero: scritta sulla scheda del prof
blu: misurata sul disegno della scheda (margine circa 5-10 cm)
rosso: ipotesi, la scheda non la dice: da chiedere al prof
Sul plastico in scala 1:100: moltiplica per 10 e leggi millimetri (1,50 m = 15 mm).

Spessore del tetto delle stanze: la scheda non lo mostra.
Sul plastico usa lo spessore del materiale, a filo del muro in cima.

Il terreno sotto la linea di taglio è solo grafico, non è una misura.

Sezione CC', scala 1:50

Taglio est-ovest lungo l'asse della casa, guardando verso sud (est a sinistra, ovest a destra). Quote in metri, pavimento = 0,00.

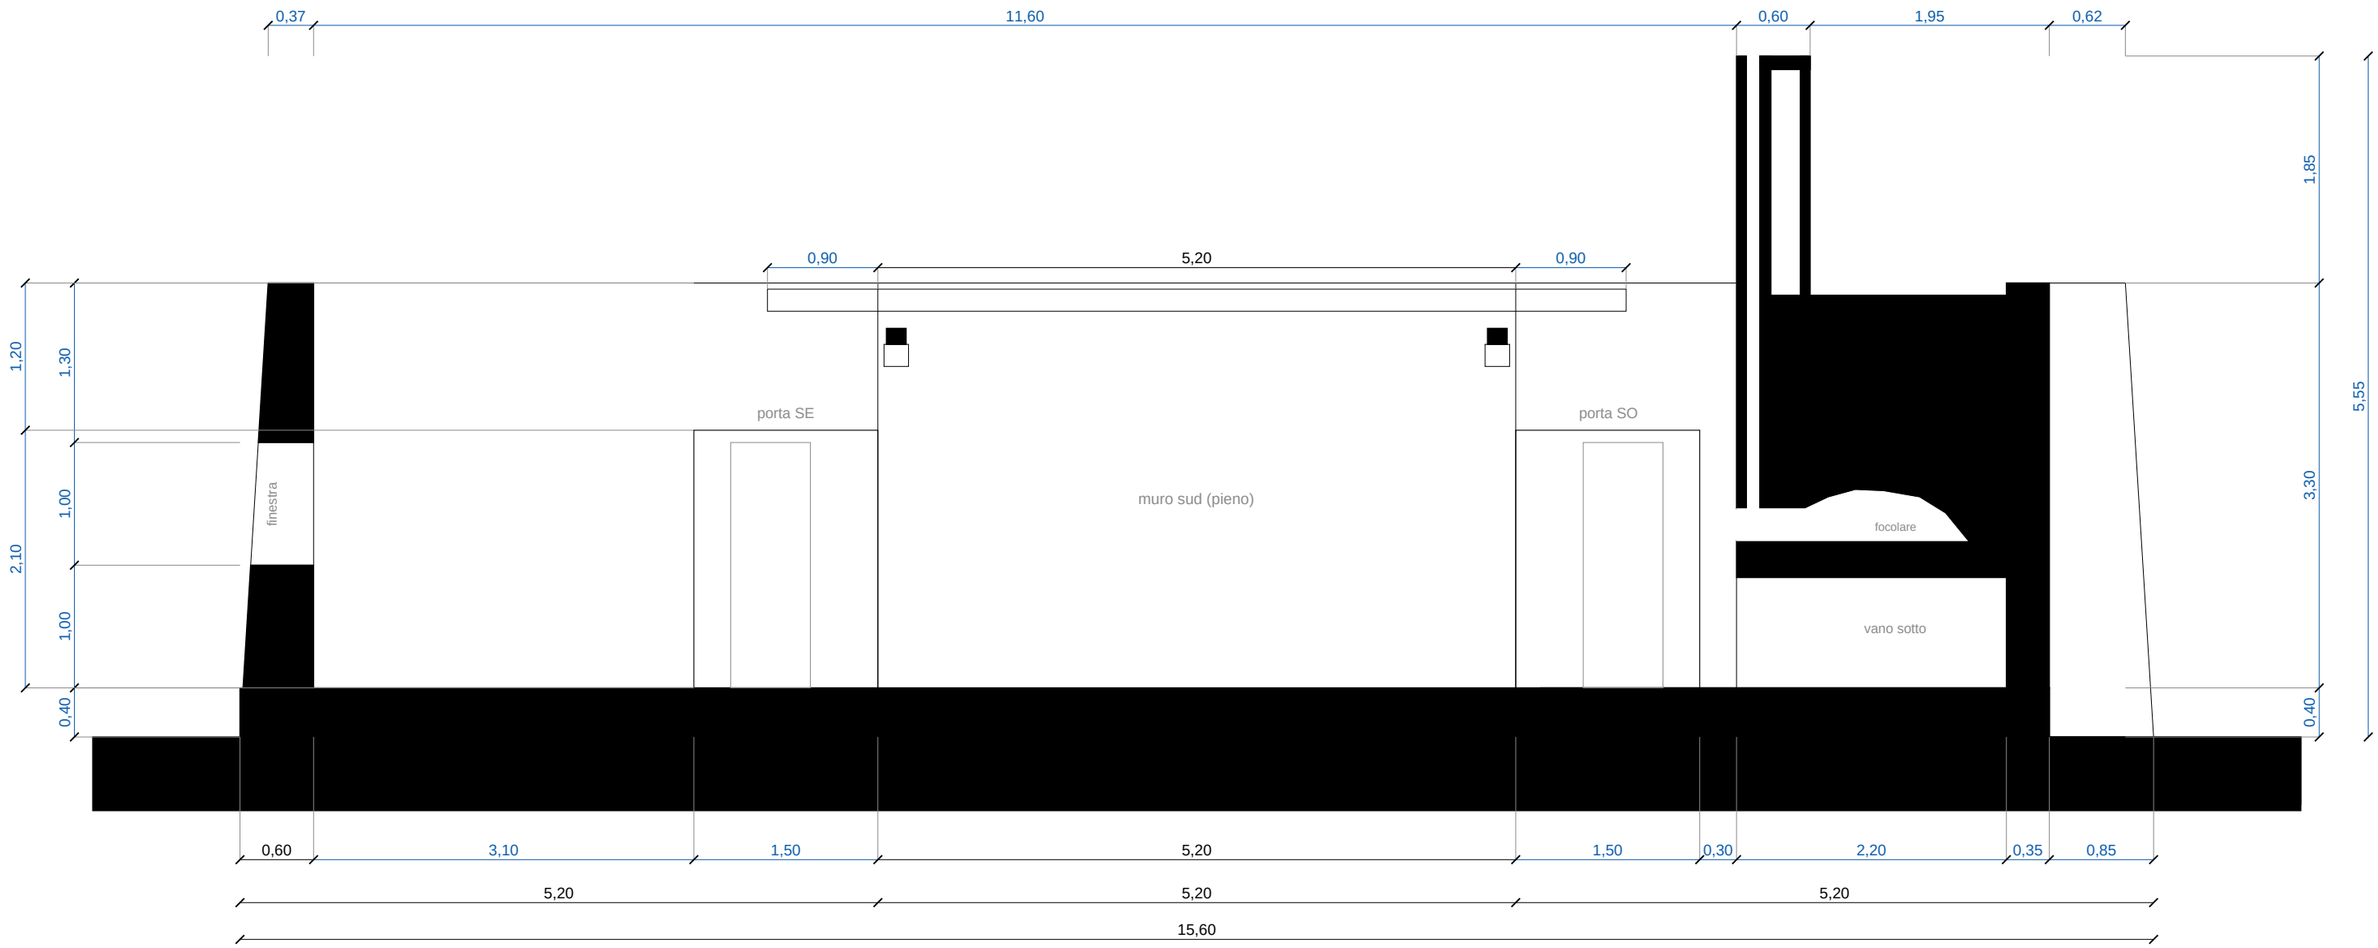

Il camino è disegnato con tutte le sue misure nella tavola 3.


Il muro esterno è inclinato: 0,60 a terra, 0,37 in cima. Sul plastico puoi farlo dritto (5-6 mm) e tenere l'altezza totale di 37 mm dal terreno.

Come leggere le quote (in metri)

nero: scritta sulla scheda del prof
blu: misurata sul disegno della scheda (margine circa 5-10 cm)
rosso: ipotesi, la scheda non la dice: da chiedere al prof
Sul plastico in scala 1:100: moltiplica per 10 e leggi millimetri (1,50 m = 15 mm).

Sezione BB' (facciata nord), scala 1:50

Vista da fuori, guardando verso sud (est a sinistra, ovest a destra). Quote in metri, terreno = -0,40, pavimento = 0,00.

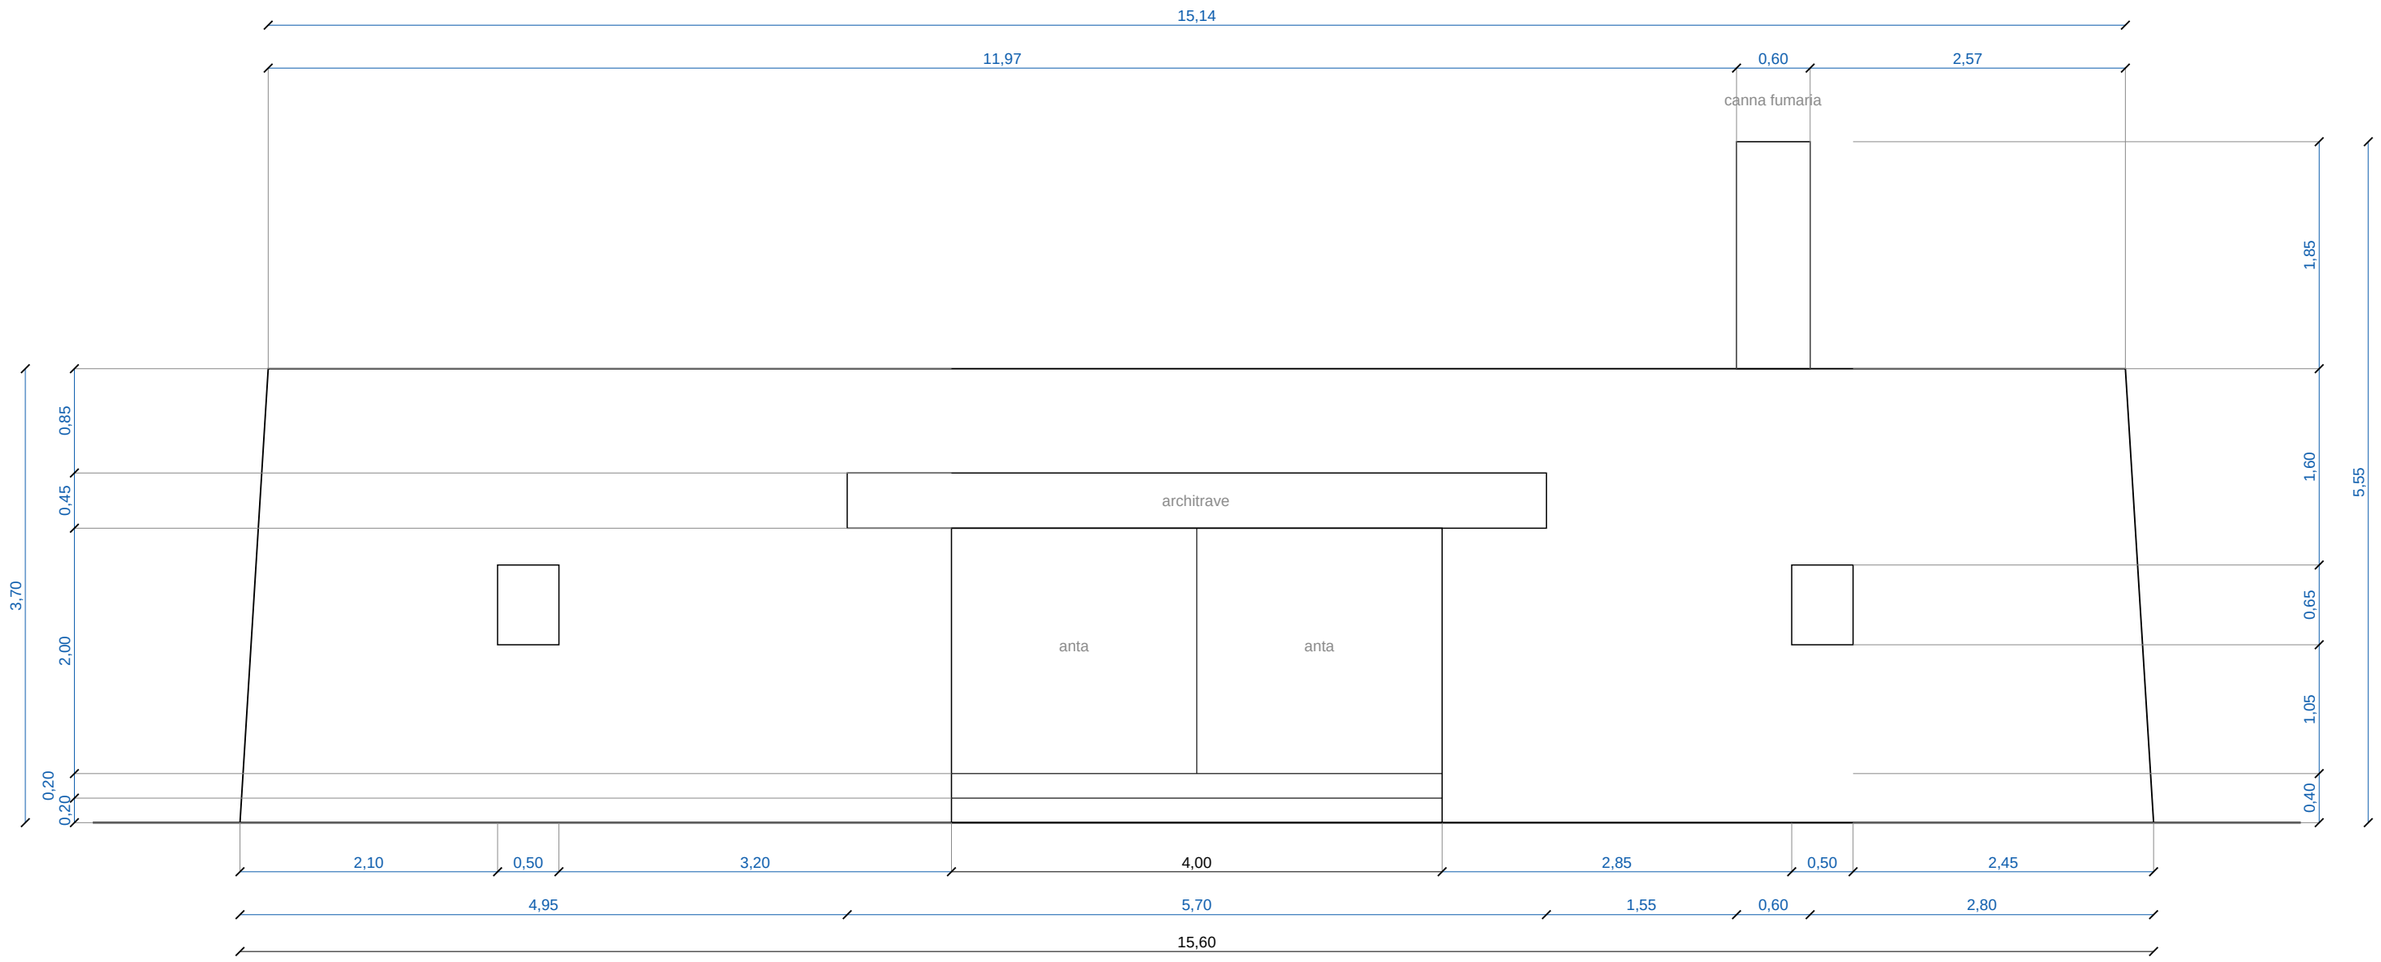

L'apertura nord è larga 4,00 e ha due ante da 2,00, alte fino a 2,00 sul pavimento.

Due gradini (0,20 ciascuno) portano dal terreno al pavimento; il gradino basso è profondo 0,60.

L'architrave di 5,70 sporge 0,85 per parte oltre l'apertura.

Come leggere le quote (in metri)

nero: scritta sulla scheda del prof

blu: misurata sul disegno della scheda (margine circa 5-10 cm)

rosso: ipotesi, la scheda non la dice: da chiedere al prof

Sul plastico in scala 1:100: moltiplica per 10 e leggi millimetri (1,50 m = 15 mm).